מינהל התכנון
הועדה הארצית לתכנון ובניה של תשתיות לאומיות

תכנית תתל/ 79 11:07:39 27/11/2024 נספח חתכים חתכים עקרוניים לאורך מסילה

תתל/ 79
המאושרת ... עפ"י החלטה תמאו/ 23
וחתומה בידי מזכיר ממשלה ובידי מזכיר הועדה
אפרת
מזכיר הועדה
23/03/2025 תאריך:
מזכיר ממשלה
תאריך:

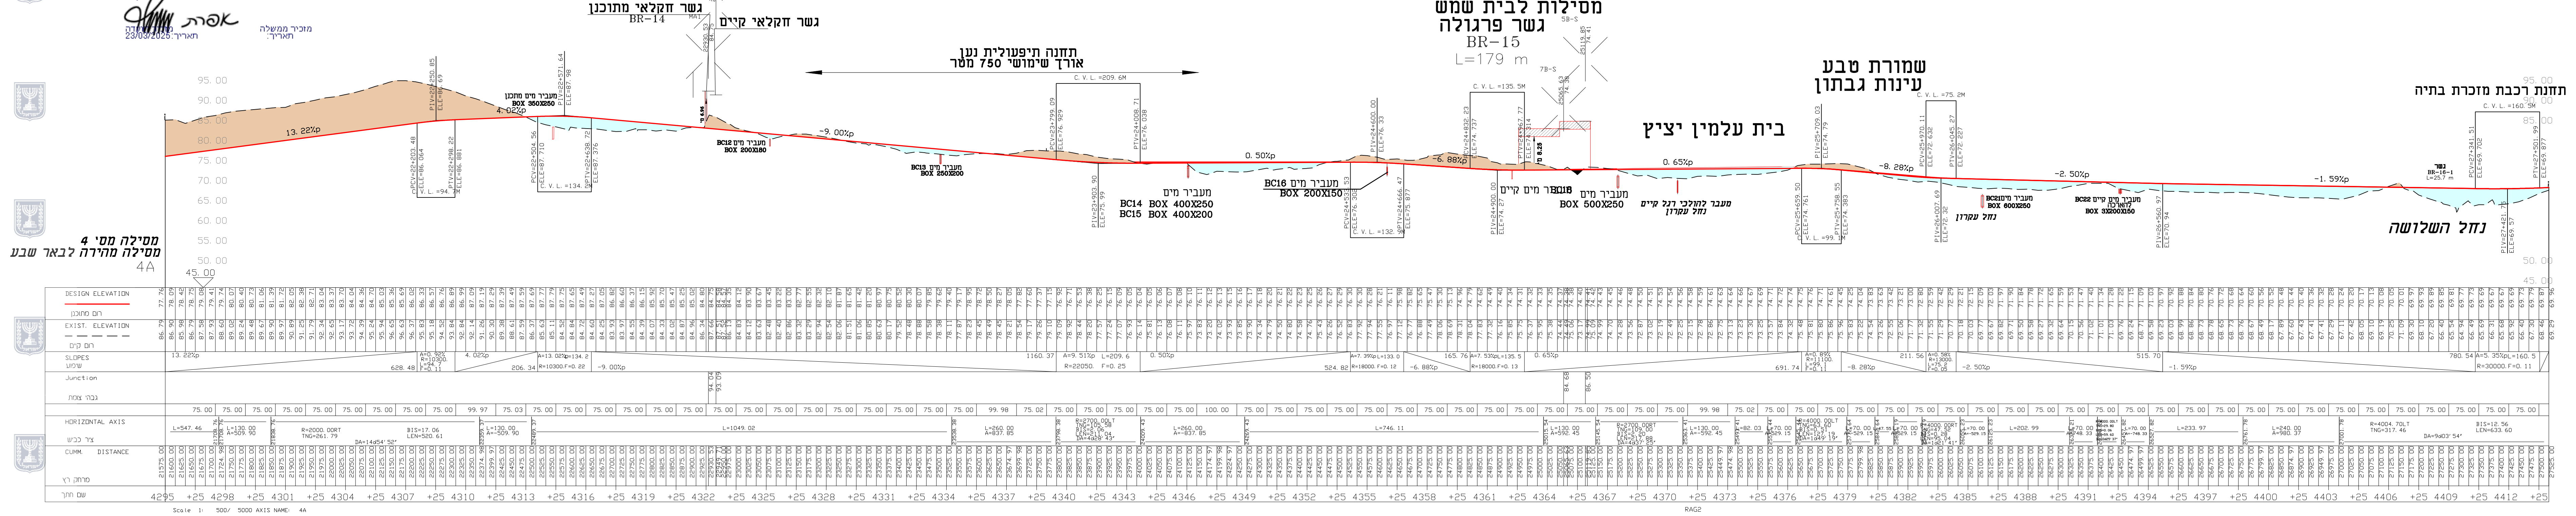
לנתב"ג
גשר חקלאי מתוכנן BR-14
גשר חקלאי קיים
תחנה תיפעולית נען
אורך שימושי 750 מטר
מסילות לבית שמש
גשר פרגולה
BR-15
L=179 m
בית עלמין יציץ
שמורת טבע
עינות גבתון
תחנת רכבת מזכרת בתיה
נחל השלושה
נחל עקרון
מעביר מים BOX 350X250
BC12 מעביר מים BOX 200X180
BC13 מעביר מים BOX 250X200
BC14 BOX 400X250
BC15 BOX 400X200
BC16 מעביר מים BOX 200X150
מעביר מים קיים
מעביר מים BOX 500X250
מעבר להולכי רגל קיים
BC21 מעביר מים BOX 600X250
BC22 מעביר מים קיים להארכה BOX 3X200X150
מסילה מס' 4
מסילה מהירה לבאר שבע
4A
13.22%p
4.02%p
-9.00%p
0.50%p
-6.88%p
0.65%p
-8.28%p
-2.50%p
-1.59%p
DESIGN ELEVATION
רום מתוכנן
EXIST. ELEVATION
רום קיים
SLOPES
שיפוע
Junction
גבהי צומת
HORIZONTAL AXIS
ציר כביש
CUMM. DISTANCE
מרחק רץ
שם חתך
Scale 1: 500/ 5000 AXIS NAME: 4A

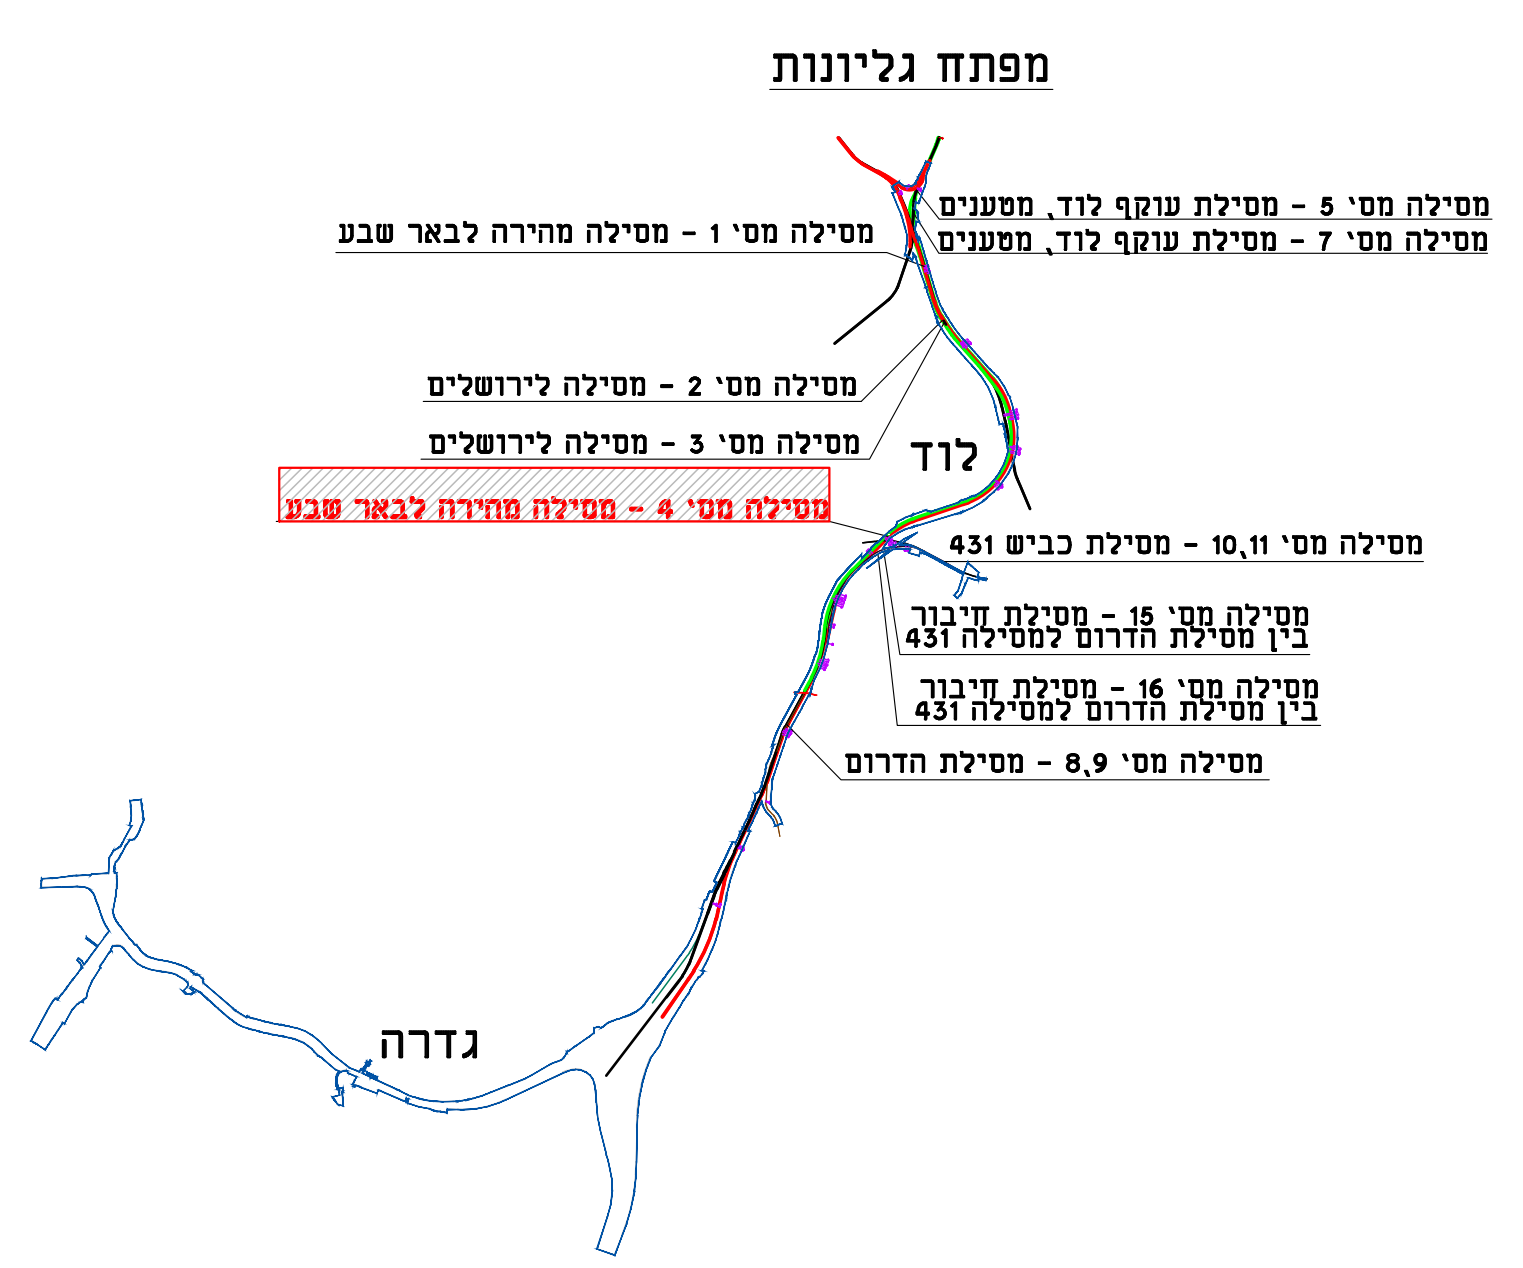
מפתח גליונות
מסילה מס' 5 - מסילת עוקף לוד, מטענים
מסילה מס' 7 - מסילת עוקף לוד, מטענים
מסילה מס' 1 - מסילה מהירה לבאר שבע
מסילה מס' 2 - מסילה לירושלים
מסילה מס' 3 - מסילה לירושלים
לוד
מסילה מס' 4 - מסילה מהירה לבאר שבע
מסילה מס' 10,11 - מסילת כביש 431
מסילה מס' 15 - מסילת חיבור בין מסילת הדרום למסילה 431
מסילה מס' 16 - מסילת חיבור בין מסילת הדרום למסילה 431
מסילה מס' 8,9 - מסילת הדרום
גדרה

חוק התכנון והבנייה, התשכ"ה – 1965	
תכנית לתשתית לאומית	
תת"ל\79	
מסילת פלשת שורק-עוקף לוד	
נספח - חתכים עקרוניים לאורך מסילה גליון 2 מתוך 7	
מחוז	דרום, מרכז, ירושלים
תאריך	10/10/24
קנה מידה	1 : 500\5000
עורך הנספח	שם: אלכס שמידט תאגיד: חסון-ירושלמי

מקרא

קטע במילוי	▨
קטע בחפירה	▨

לבאר שבע

לתל אביב
לנתב"ג
גשר BR-06-4 L=83.0
גשר BR-07 L=165 m
BOX BR-08 L=22 m
גשר BR-09 L=110 m
כביש 443
נחל אילון
כביש לאחיסמך
מסילה קיימת לירושלים A1
רום מסילה A1
מסילה מתוכננת ציר 7
מנהרה (מעבר תת קרקעי) TU-6 L=153 m
מנהרה (מעבר תת קרקעי) TU-9 L=128 m
מנהרה TU-12
מסילה מתחם רג"מ
נחל דניאל קיים
נחל אילון מתוכנן
נחל אילון קיים
הסדרת נחל אילון
דרך קיימת "נשר"
מנהרה L=5700 מ'
10.47
3.75
7.34
0.00%p
-6.10%p
1.85%p
4.00%p
7.94%p
13.22%p
מסילה מס' 4
מסילה מהירה לבאר שבע
4A
Scale 1: 500/ 5000 AXIS NAME: 4A

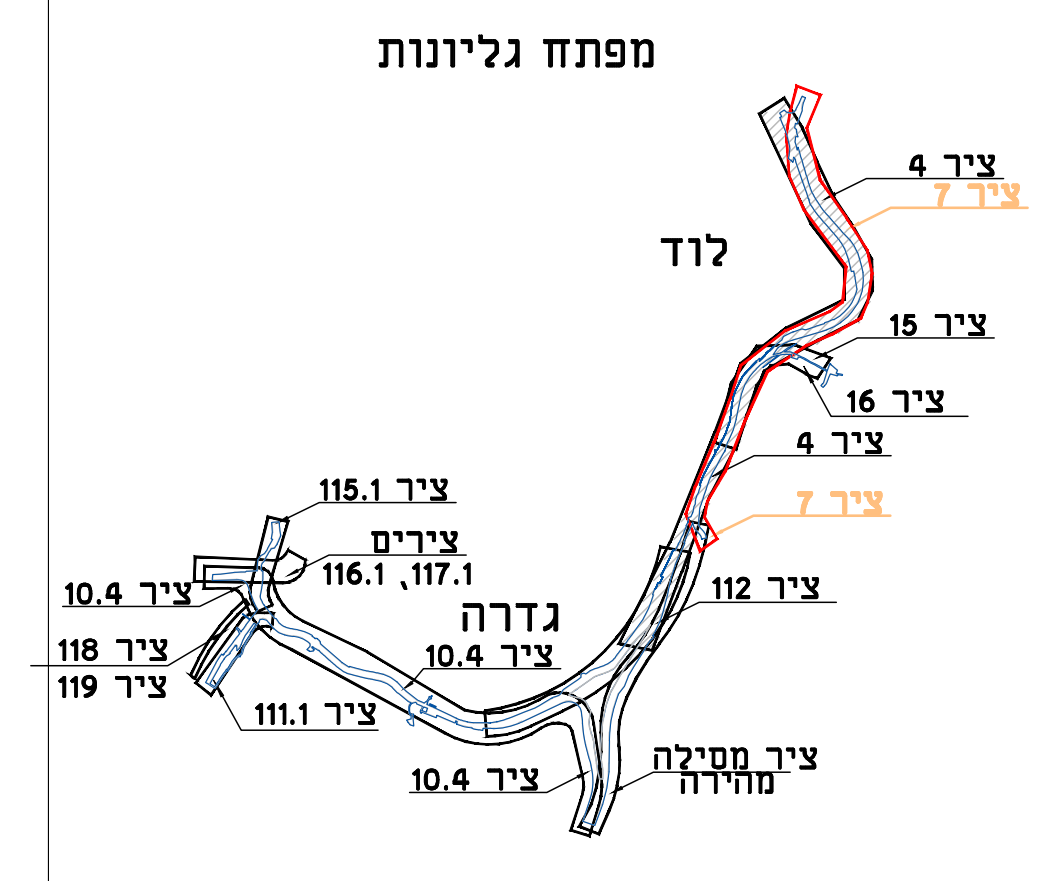
מפתח גליונות
לוד
ציר 4
ציר 7
ציר 15
ציר 16
ציר 4
ציר 7
ציר 115.1
צירים 116.1, 117.1
ציר 10.4
ציר 112
גדרה
ציר 10.4
ציר 118
ציר 119
ציר 111.1
ציר 10.4
ציר מסילה מהירה

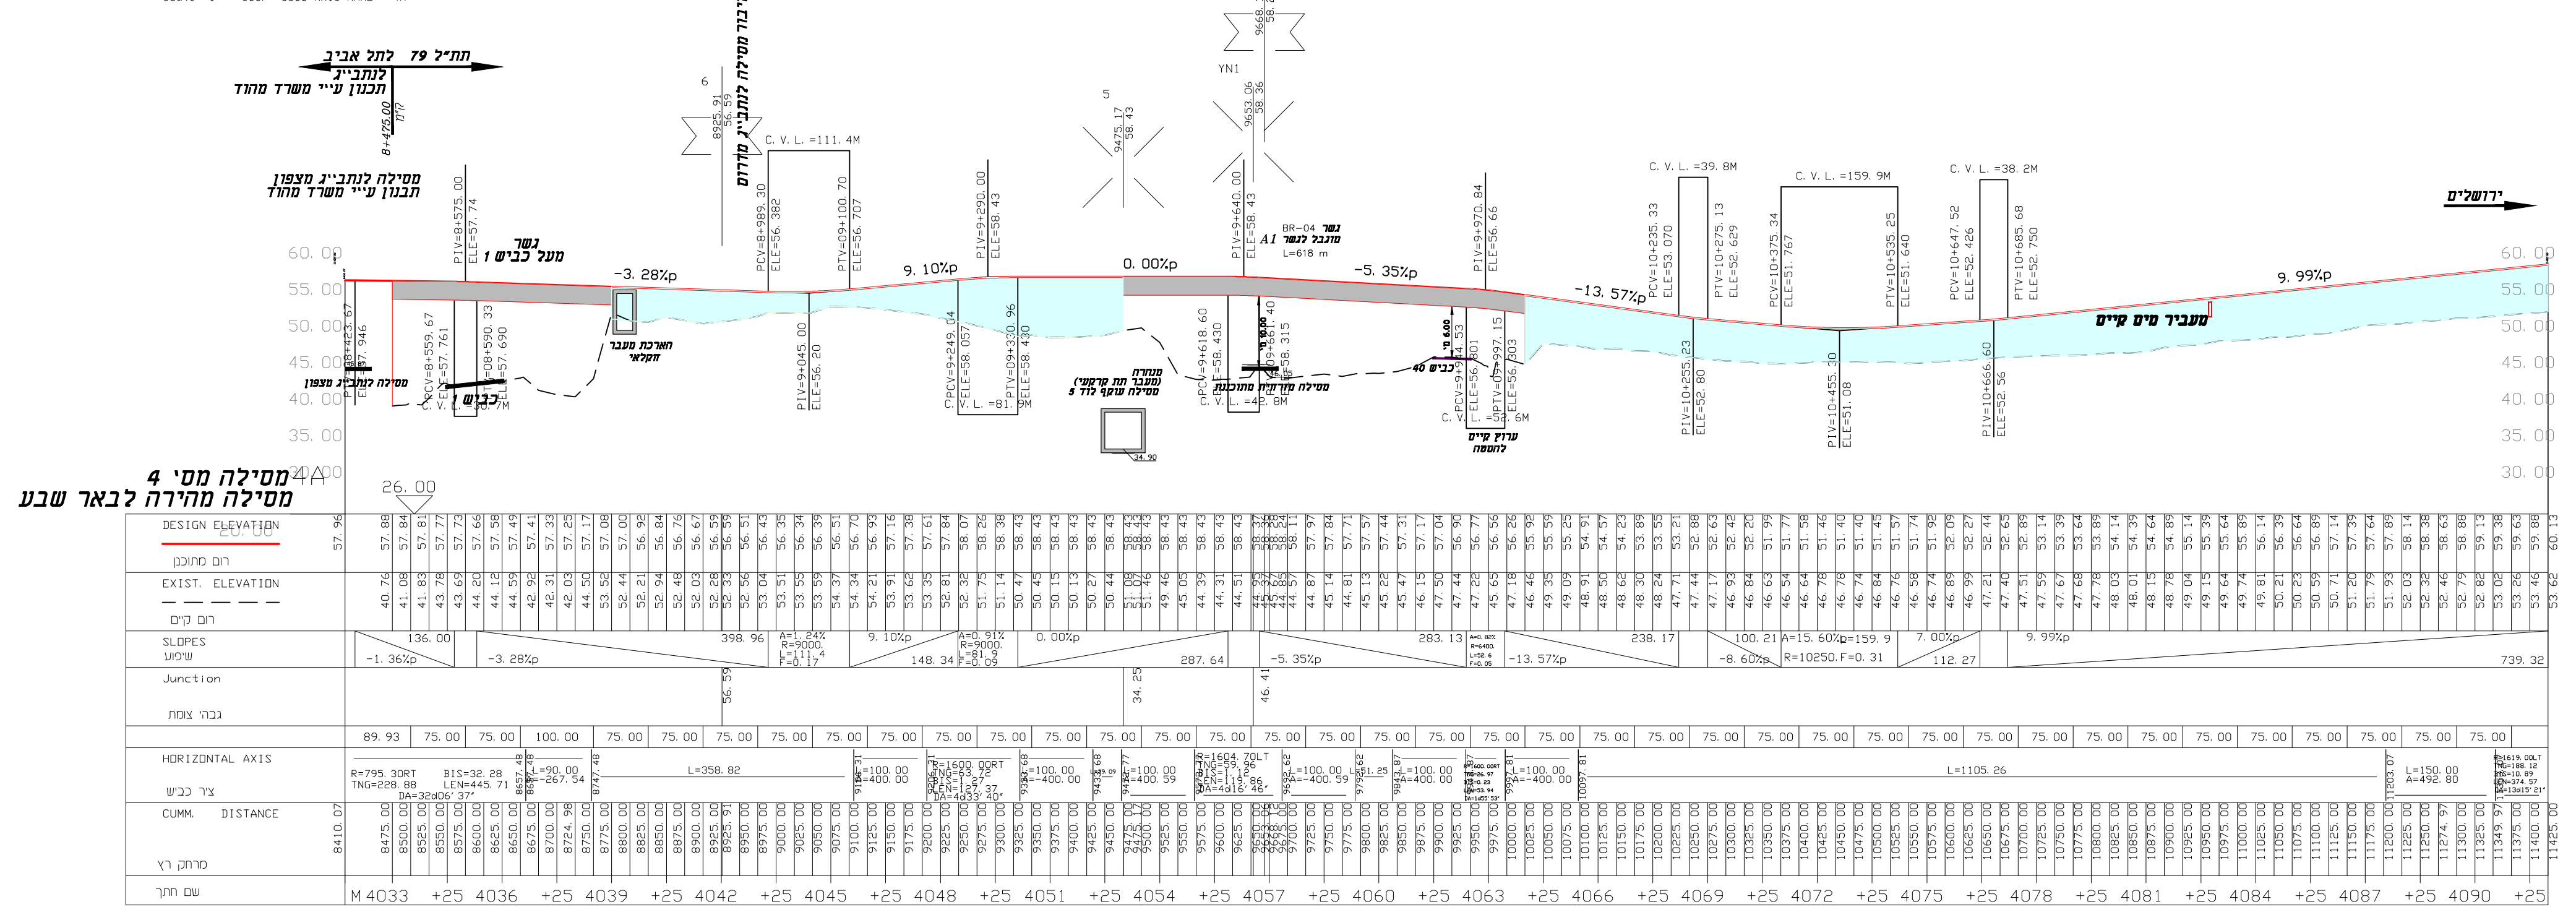
תת"ל 79 לתל אביב לנתב"ג
תכנון ע"י משרד מהוד
מסילה לנתב"ג מצפון תכנון ע"י משרד מהוד
חיבור מסילה לנתב"ג מדרום
ירושלים
גשר מעל כביש 1
הארכת מעבר חקלאי
גשר BR-04 מתוכנן לגשר A1 L=618 m
מנהרה (מעבר תת קרקעי) מסילת עוקף לוד 5
מסילה מהירה מתוכננת
כביש 40
ערוץ קיים להסטה
מעביר מים קיים
-3.28%p
9.10%p
0.00%p
-5.35%p
-13.57%p
9.99%p
מסילה מס' 4
מסילה מהירה לבאר שבע
4A

רכבת ישראל

חסון•ירושלמי תכנון
תכנון הנדסה אזרחית
דרכים, מסילות ברזל, תנועה, ניקוז, קונסטרוקציה

מהוד הנדסה בע"מ
באר - שבע, בית בלטש, יהודה הנחתום 4
טל. 08-6288060 פקס. 08-6288070
תל - אביב, מגדלי סוויסה, רח' יגאל אלון 65
טל. 03-6251188 פקס. 03-6251187