מינהל התכנון

הועדה הארצית לתכנון ובניה של תשתיות לאומיות

תכנית תתל/ 79 19/11/2024 17:30:58 נספח חתכים חתכים עקרוניים לאורך

תתל/ 79 'תכנית לתשתית לאומית מס

המאושרות ע"י הממשלה לפי החלטה תמא/ 23

12/02/2025מיום

וחתומה בידי מזכיר ממשלה ובידי מזכיר הועדה

אפרת

מזכיר הועדה　　　　מזכיר ממשלה

23/03/2025:תאריך　　　　תאריך:

ציר 10.4-1

ציר 10.4-1

מקרא

קטע במילוי	🟦
קטע בחפירה	🟫

ציר 10.4-2 אזור חיבור למסילה קיימת נען-באר שבע

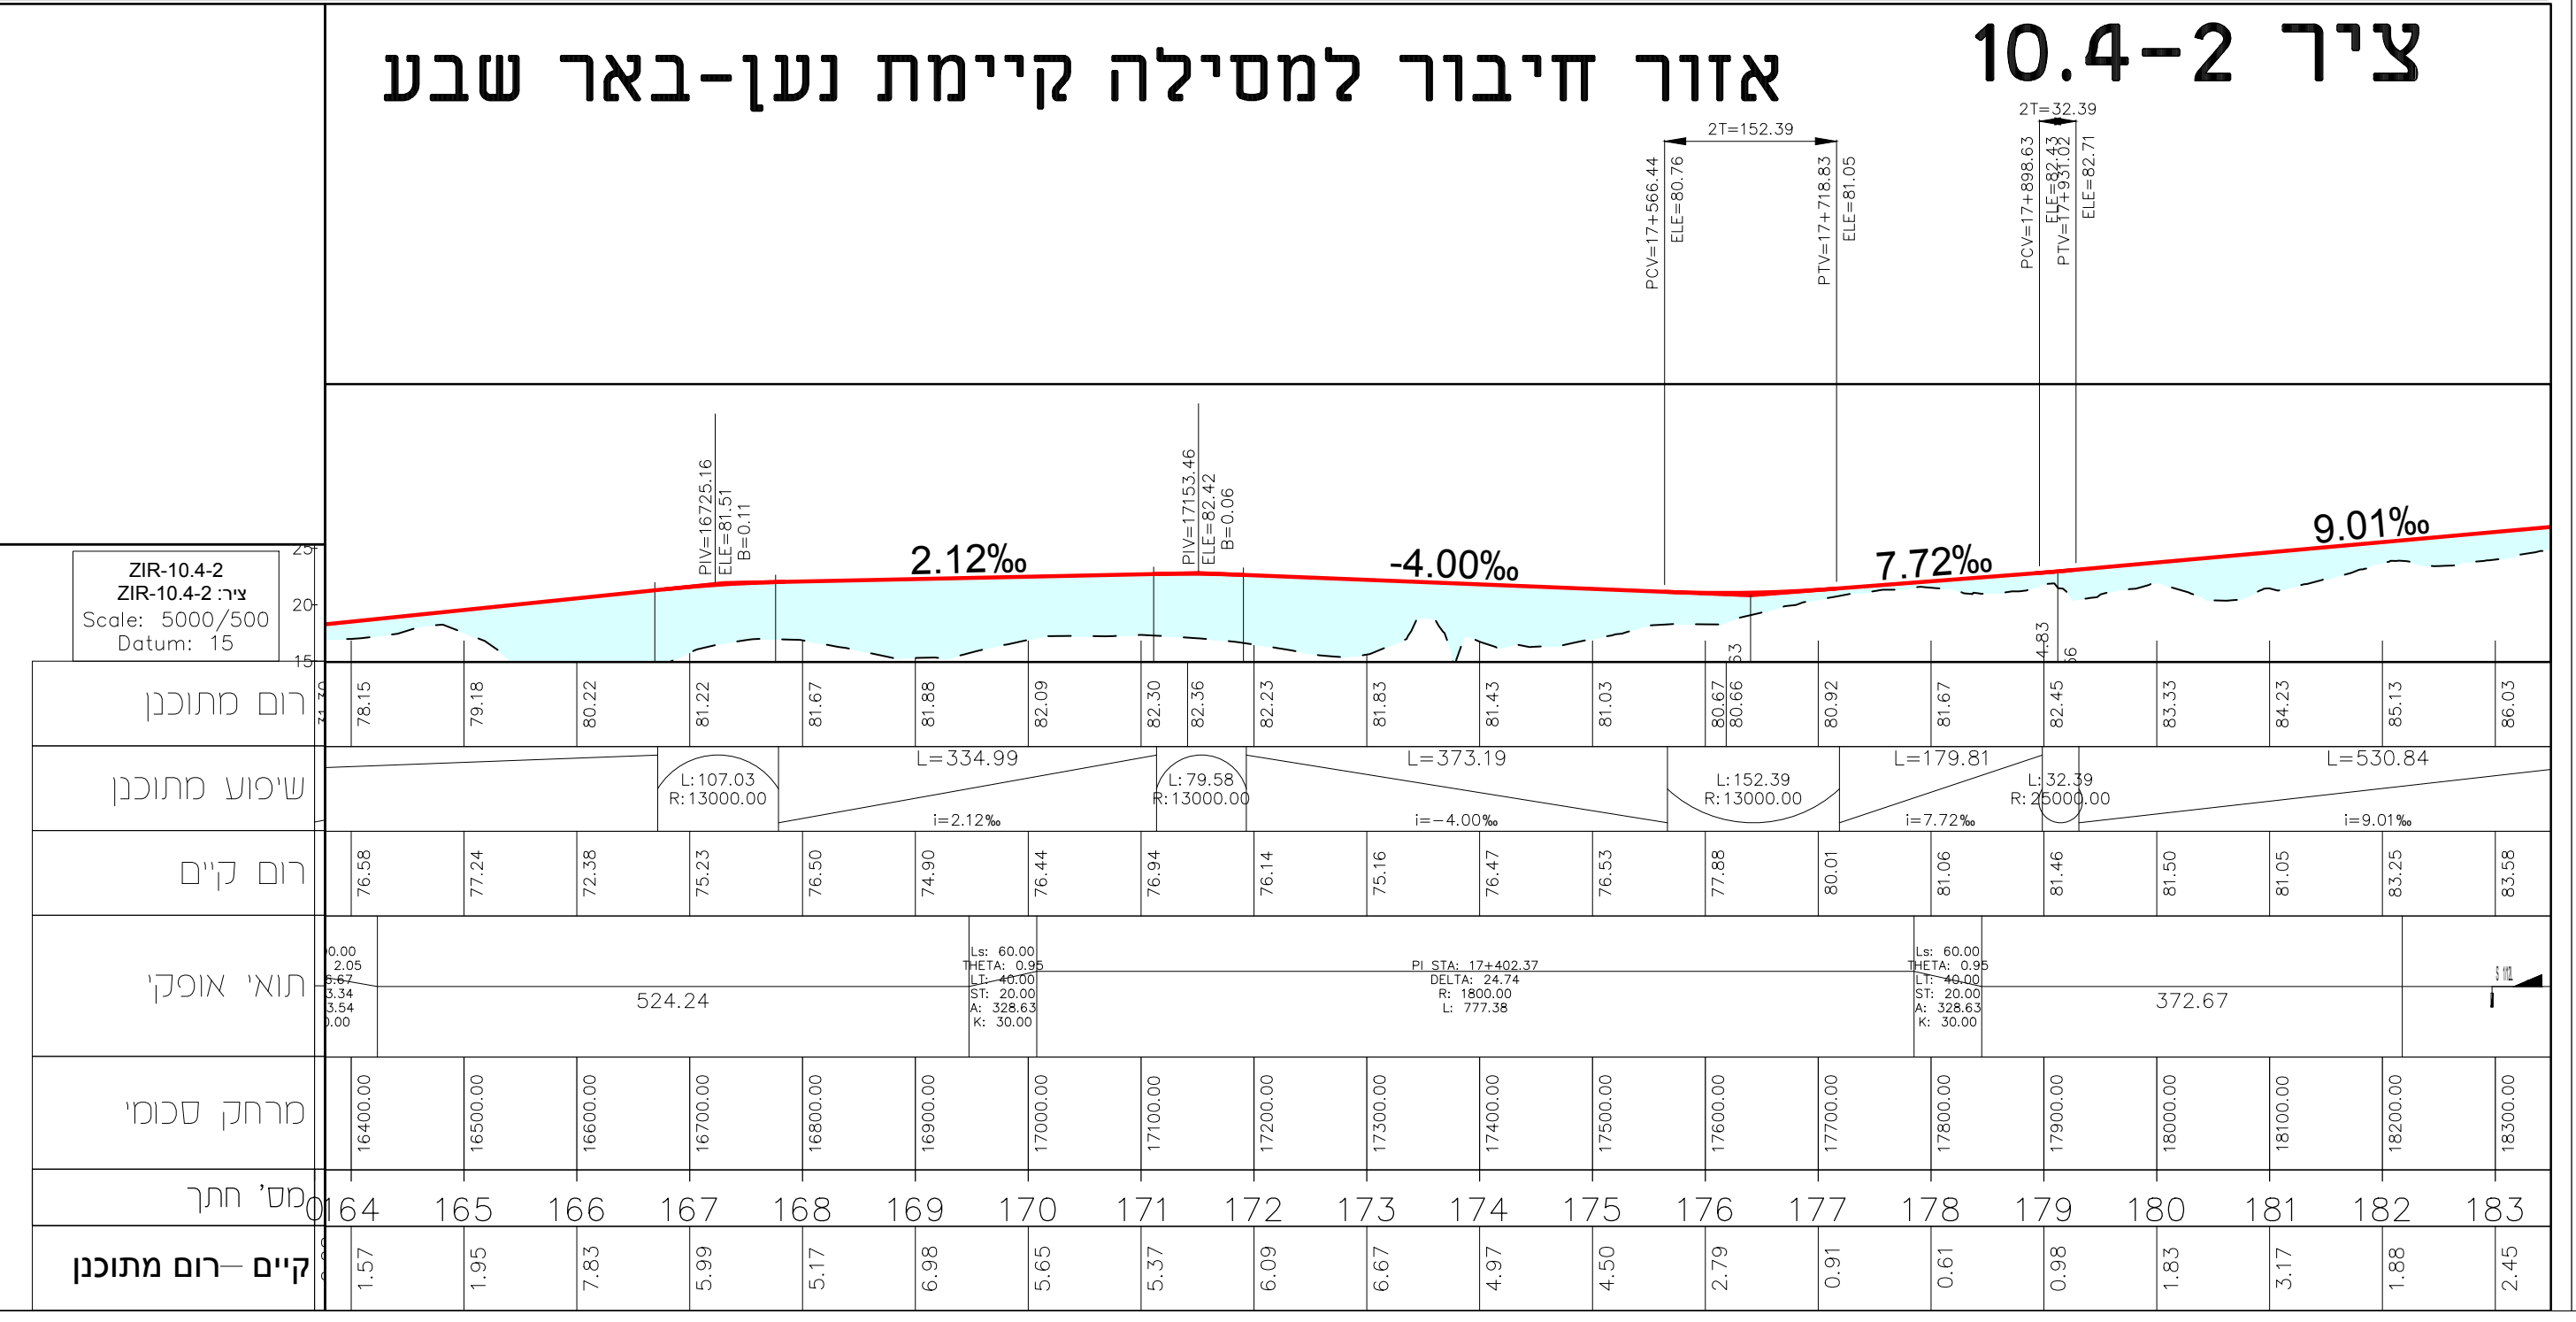

חוק התכנון והבנייה, התשכ"ה - 1965
תכנית לתשתית לאומית

תת"ל\79

מסילת פלשת שורק-עוקף לוד

נספח - חתכים עקרוניים לאורך מסילה גליון 4 מתוך 7

מחוז	מרכז, דרום, ירושלים
תאריך	22/09/2024
קנה מידה	1 : 500\5000
עורך הנספח	שם: אלי קוגלר תאגיד: מהוד הנדסה בע"ם

מפתח גליונות