מינהל התכנון
הועדה הארצית לתכנון ובניה של תשתיות לאומיות
תכנית תתל/ 79 27/11/2024 11:06:57 נספח חתכים חתכים עקרונים לאורך מסילה

תתל/ 79
'תכנית לתשתית לאומית מס
המאושרות ע"י הממשלה לפי החלטה תמאמ/ 23
מיום12/02/2025
וחתומה בידי מזכיר ממשלה ובידי מזכיר הועדה
אפרת
מזכיר הועדה
תאריך:23/03/2025
מזכיר ממשלה
תאריך:

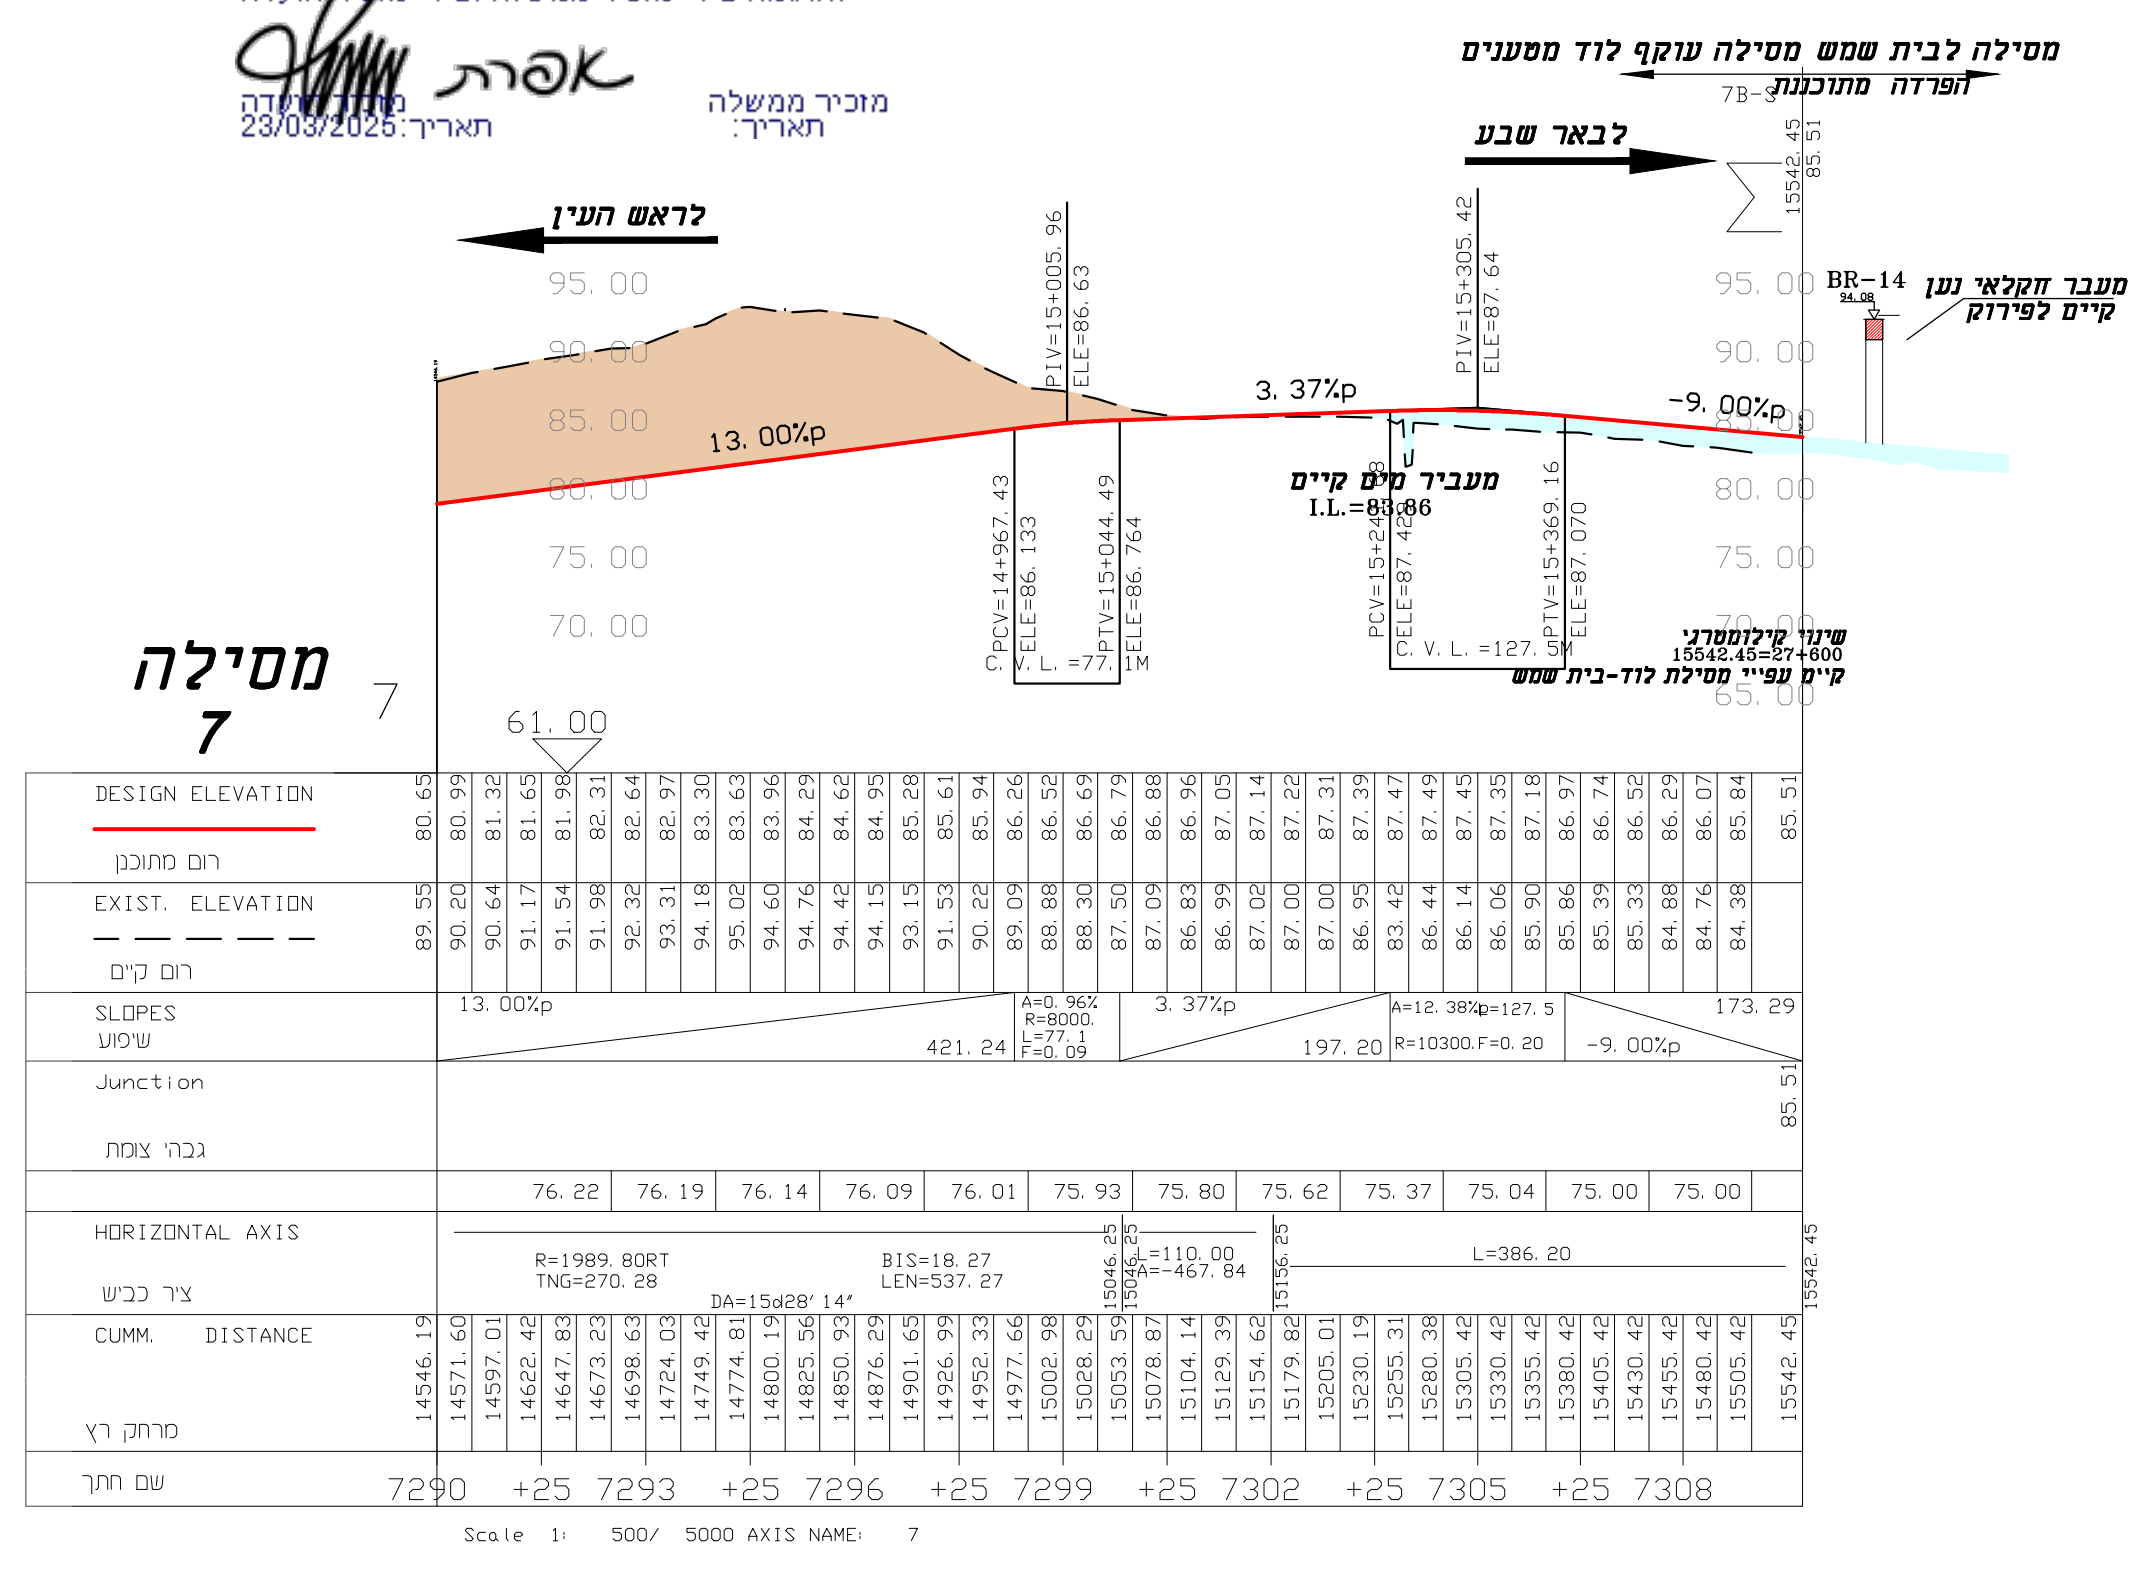

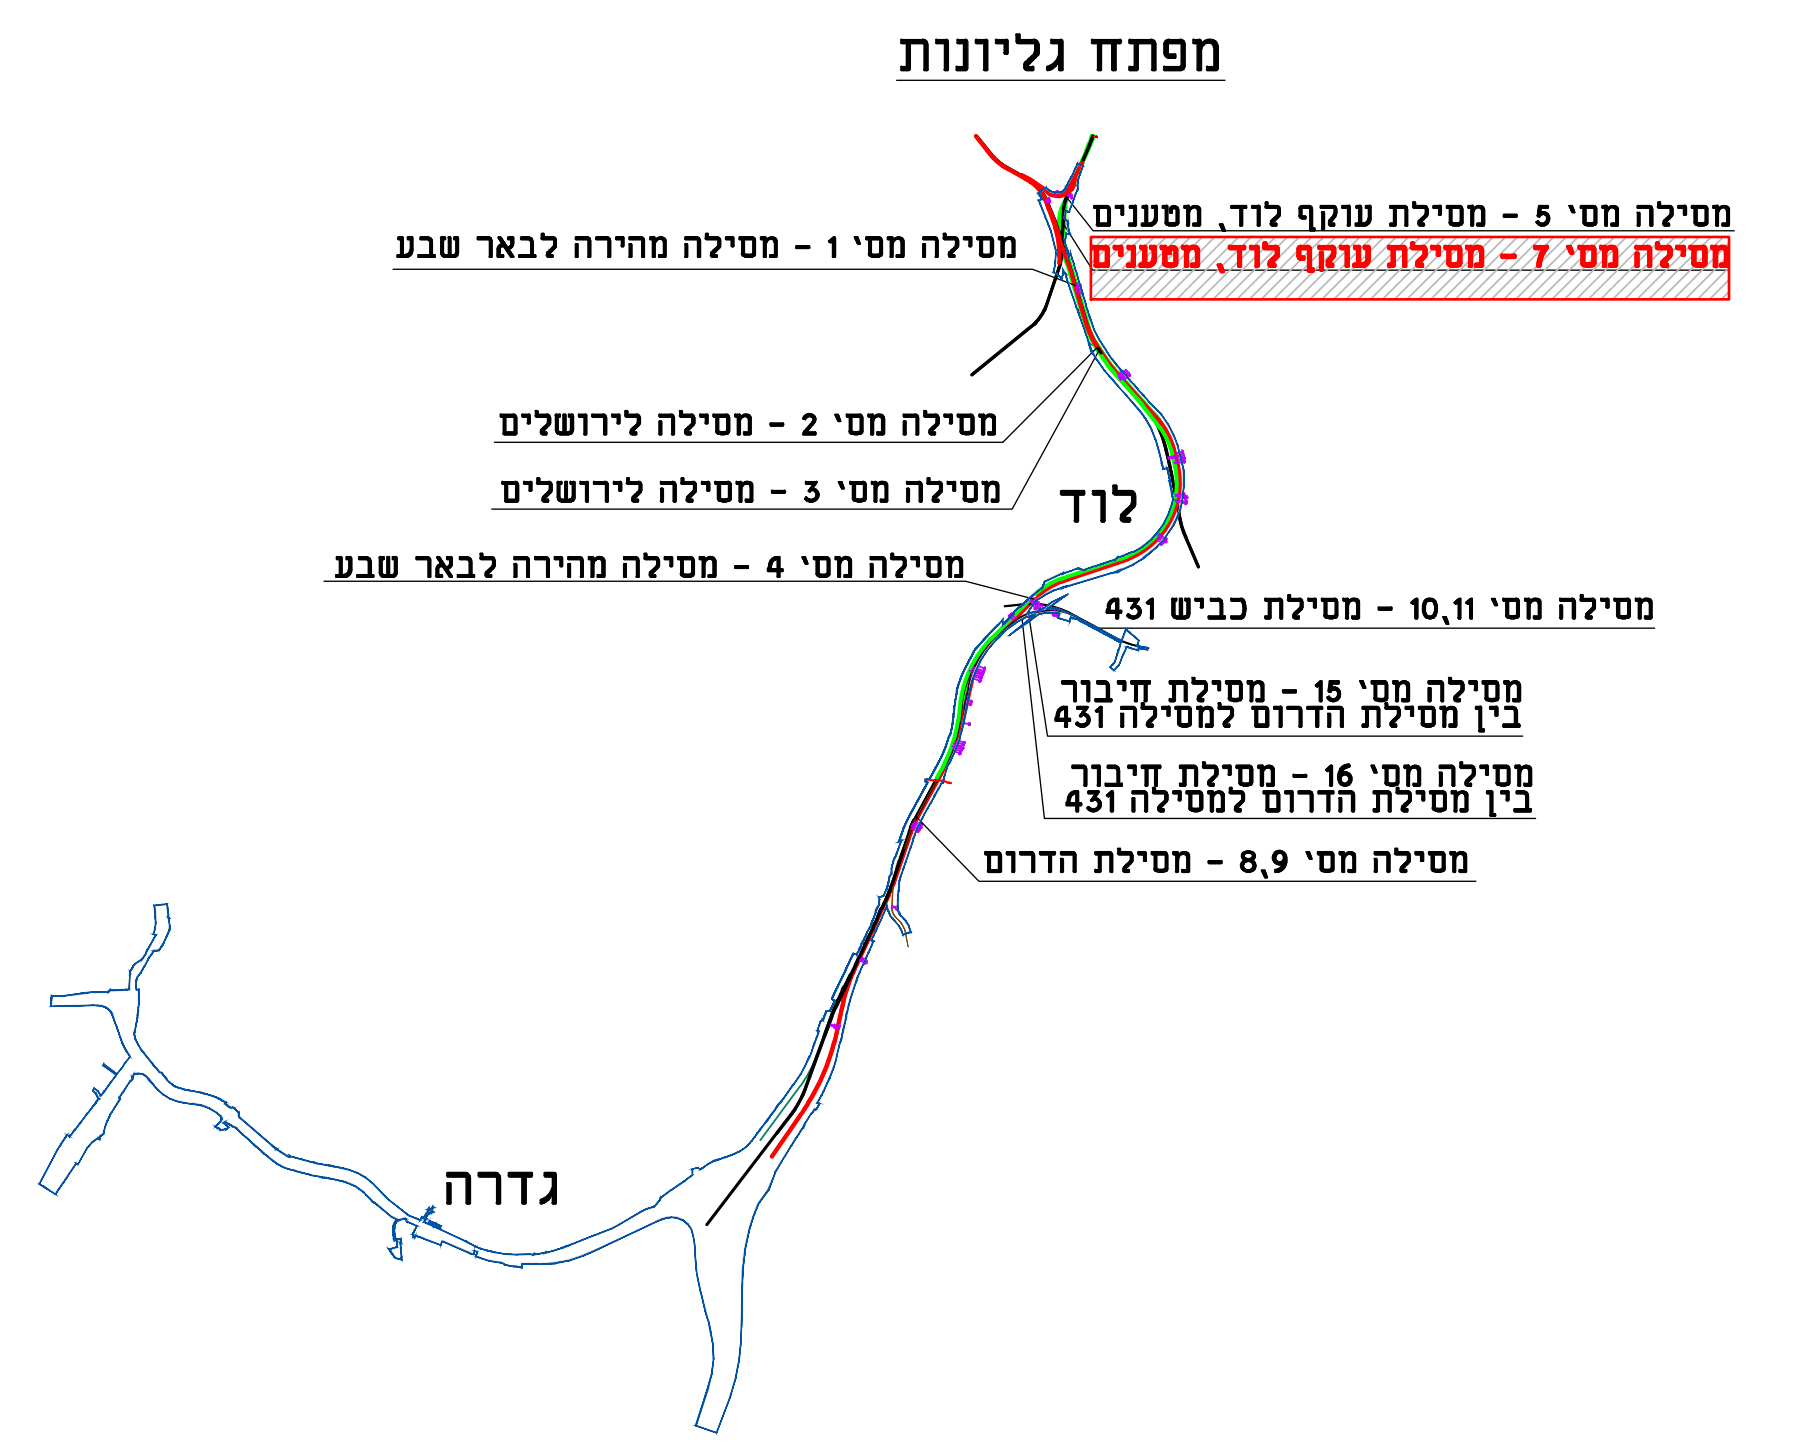
מפתח גליונות
מסילה מס' 5 - מסילת עוקף לוד, מטענים
מסילה מס' 7 - מסילת עוקף לוד, מטענים
מסילה מס' 1 - מסילה מהירה לבאר שבע
מסילה מס' 2 - מסילה לירושלים
מסילה מס' 3 - מסילה לירושלים
לוד
מסילה מס' 4 - מסילה מהירה לבאר שבע
מסילה מס' 10,11 - מסילת כביש 431
מסילה מס' 15 - מסילת חיבור
בין מסילת הדרום למסילה 431
מסילה מס' 16 - מסילת חיבור
בין מסילת הדרום למסילה 431
מסילה מס' 8,9 - מסילת הדרום
גדרה

מקרא

קטע במילוי	🟦
קטע בחפירה	🟫

חוק התכנון והבנייה, התשכ"ה - 1965
תכנית לתשתית לאומית

תת"ל\79

מסילת פלשת שורק-עוקף לוד

נספח - חתכים עקרונים לאורך מסילה גליון 1 מתוך 7

מחוז	דרום, מרכז, ירושלים
תאריך	10/10/24
קנה מידה	1 : 500\5000
עורך הנספח	שם: אלכס שמידט תאגיד: חסון-ירושלמי

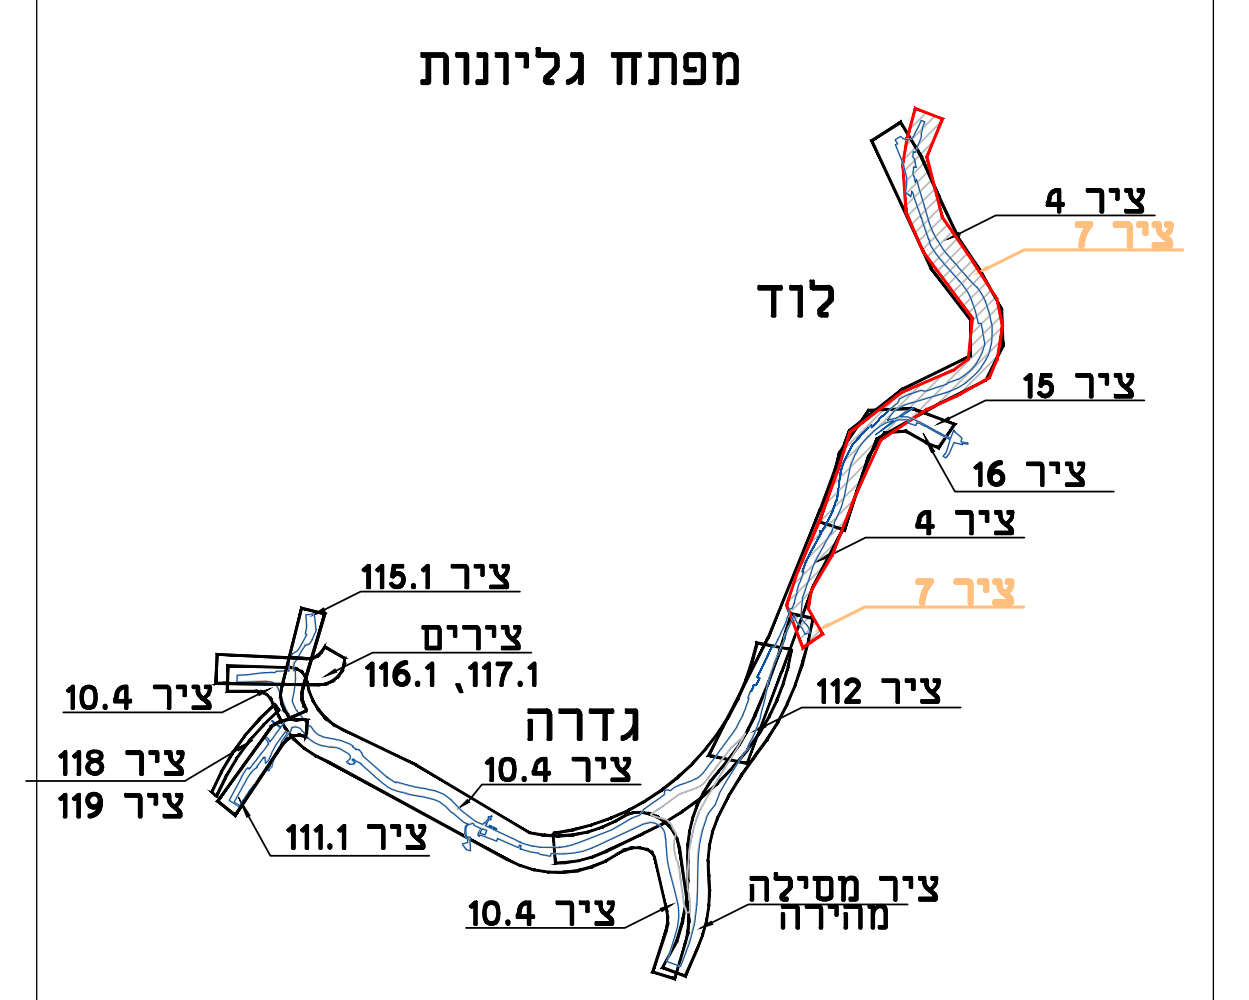

רכבת ישראל

חסון•ירושלמי תכנון
תכנון הנדסה אזרחית
דרכים, מסילות ברזל, תנועה, ניקוז, קונסטרוקציה
גדעון ירושלמי•אורן ירושלמי•הראל נחושתאי

מהוד הנדסה בע"מ
באר - שבע, **בית בלטק**, יהודה הנחתום 4
טל. 08-6288060 פקס. 08-6288070
תל - אביב, מגדלי טויוטה, רח' יגאל אלון 65
טל. 03-6251188 פקס. 03-6251187