תכנית תתל/ 65/ א 14/08/2023 11:17:22 נספח תנוחה 2.2.2 תנוחה, ניקוז וחתך לאורך

מינהל התכנון
הועדה הארצית לתכנון ובניה של תשתיות לאומיות
חוק התכנון והבניה, התשכ"ה
'תכנית לתשתית לאומית מס תתל/ 65/ א
המאושרות ע"י הממשלה לפי החלטה
מיום12/12/2022
וחתומה בידי מזכיר ממשלה ובידי מזכירת הועדה
אפרת
מזכירת הועדה — תאריך:10/01/2024
מזכיר ממשלה — תאריך:

תנוחה עייר מצב קיים

קנ״מ 1:2500

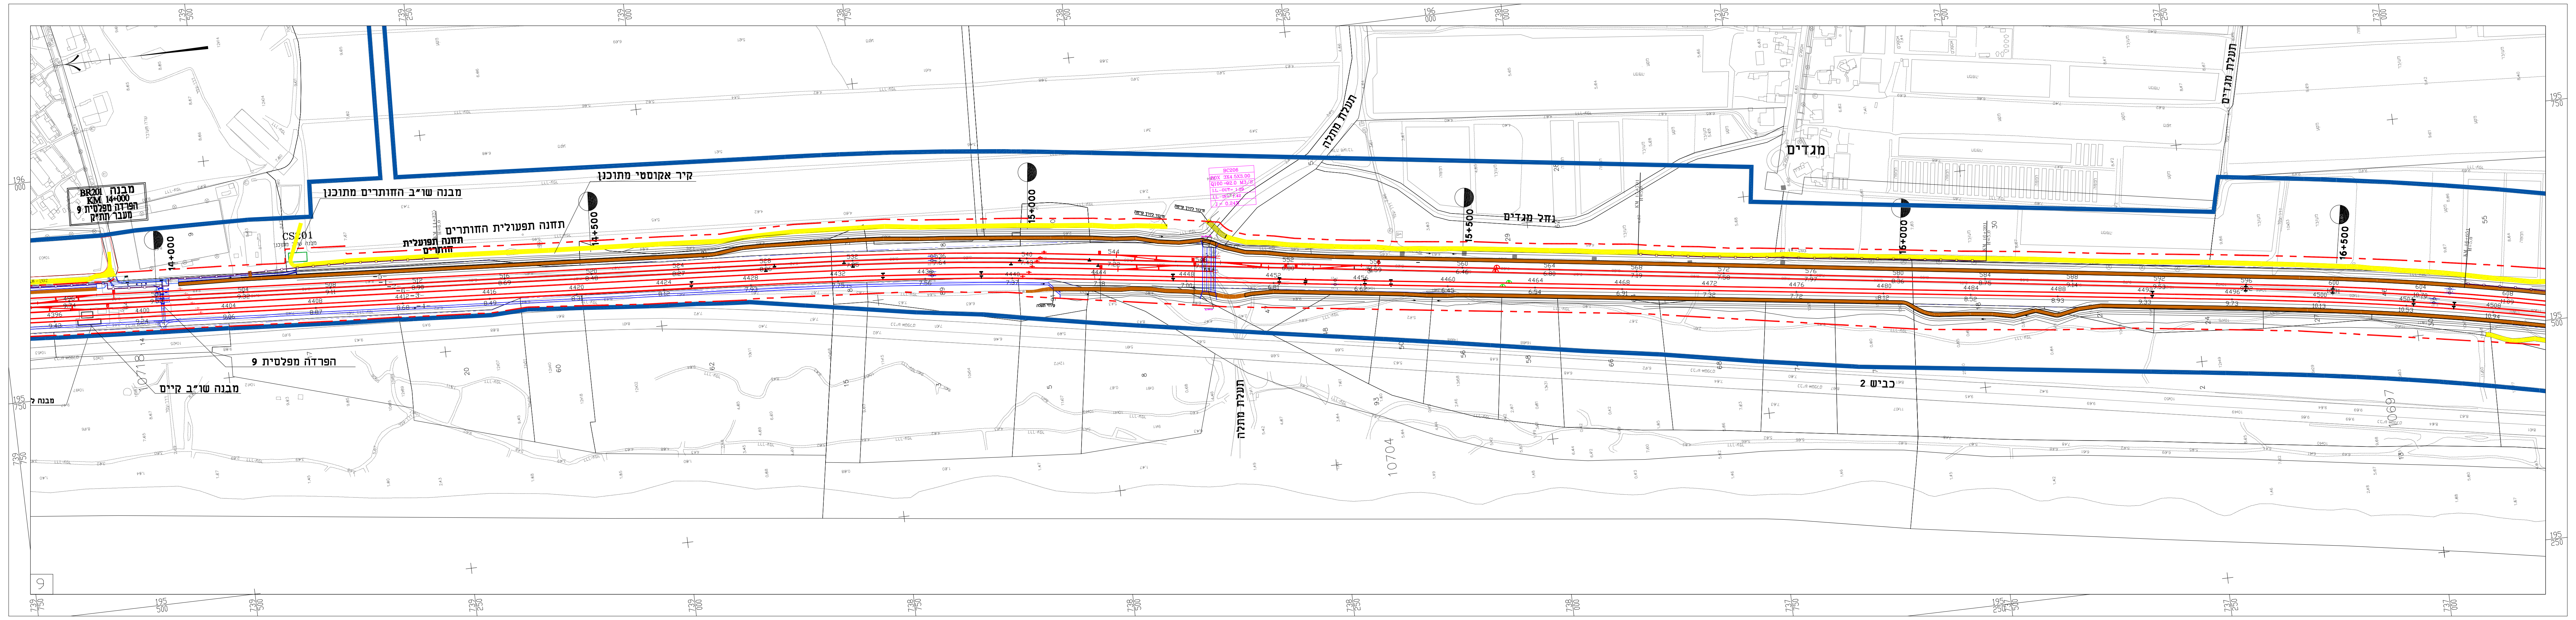

חתך לאורך מסילות פרבריות

קנ״מ 1:250\2500

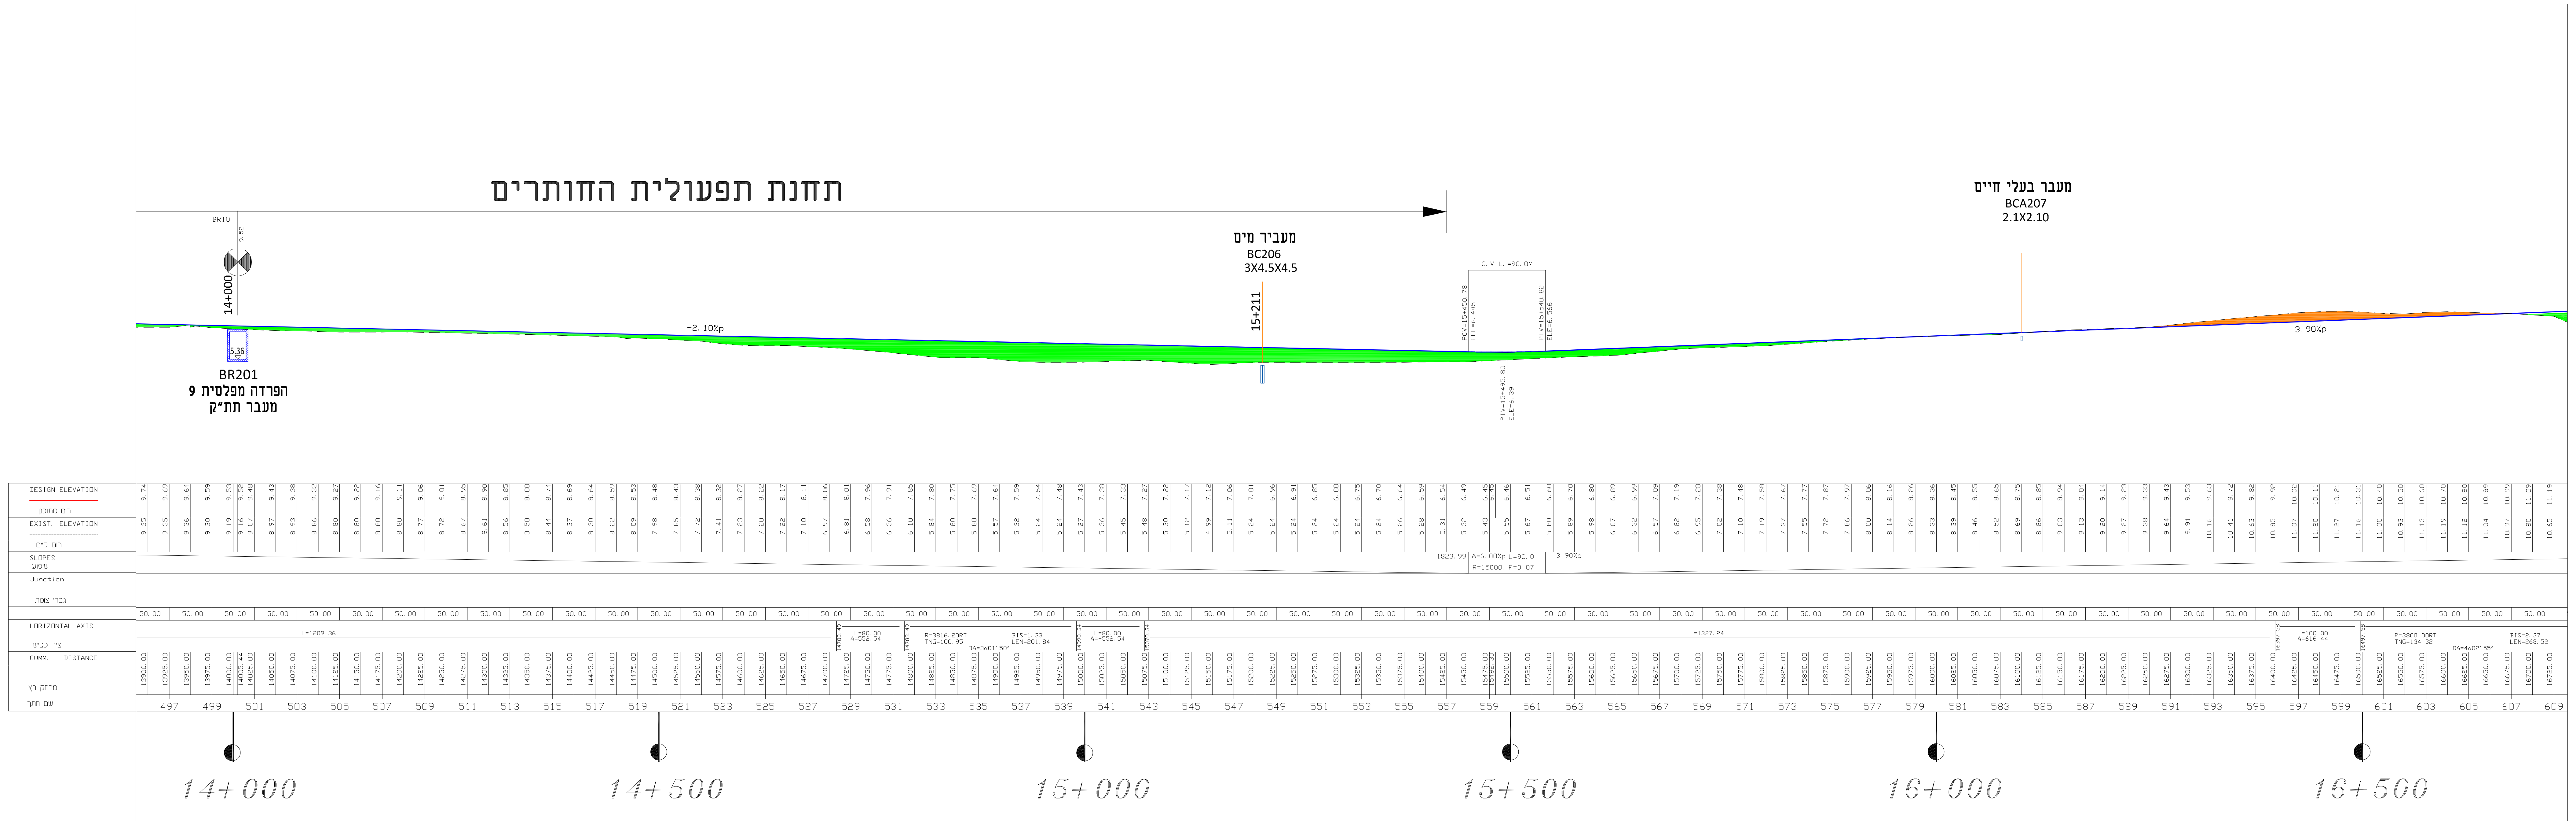

מקרא

גבול תכנית	━
גבול רצועת רכבת מוצע	━··
גבול רצועת רכבת קיים	━··
גבול שטח שיפוט	━·━
ציר מסילה מתוכננת	─
ציר מסילה קיים	─
מסילה מתוכננת בפרויקט משיק	─
מסילה ננטשת	─
קילומטר מסילה/ חתך	◐ 20+000
תחנת נוסעים מוצעת-מבנה/רציפים	▨
גשר רכבת	
גשר כביש	
מנהרת רכבת/רכב	🟨
מעבר תחתי	🟦
עתיקות	⬚
כיווני זרימה בתעלת ניקוז	←
מעביר מים מתוכנן	
מבנה שליטה ובקרה קיים- שו״ב	☐
מבנה שליטה ובקרה מתוכנן- שו״ב	🟩
מבנה תחנת השנאה תת״ל 18 - תה״ר	🟧
מבנה חישמול מתוכנן	🟦
שטח התארגנות	▨
קיר מתוכנן	━
קיר אקוסטי קיים	
קיר אקוסטי מתוכנן	
גדר מתוכננת	
מפלג	
דרך קיימת	
דרך מתוכננת	
דרך שירות	🟫
דרך חקלאית	🟨
גבול גוש ומספרו	6565
גבול חלקה ומספרה	86
מספר הדרך קווי בנין רוחב הדרך	
גבול תכנון	גבול תכנון ק״מ 3+557 ק״מ 3+508
חתך לאורך	
מסילה מתוכננת	─
רום קרקע קיימת	- - -
חפירה	🟧
מילוי	🟩

תרשים סביבה

קנ״מ 1:100000

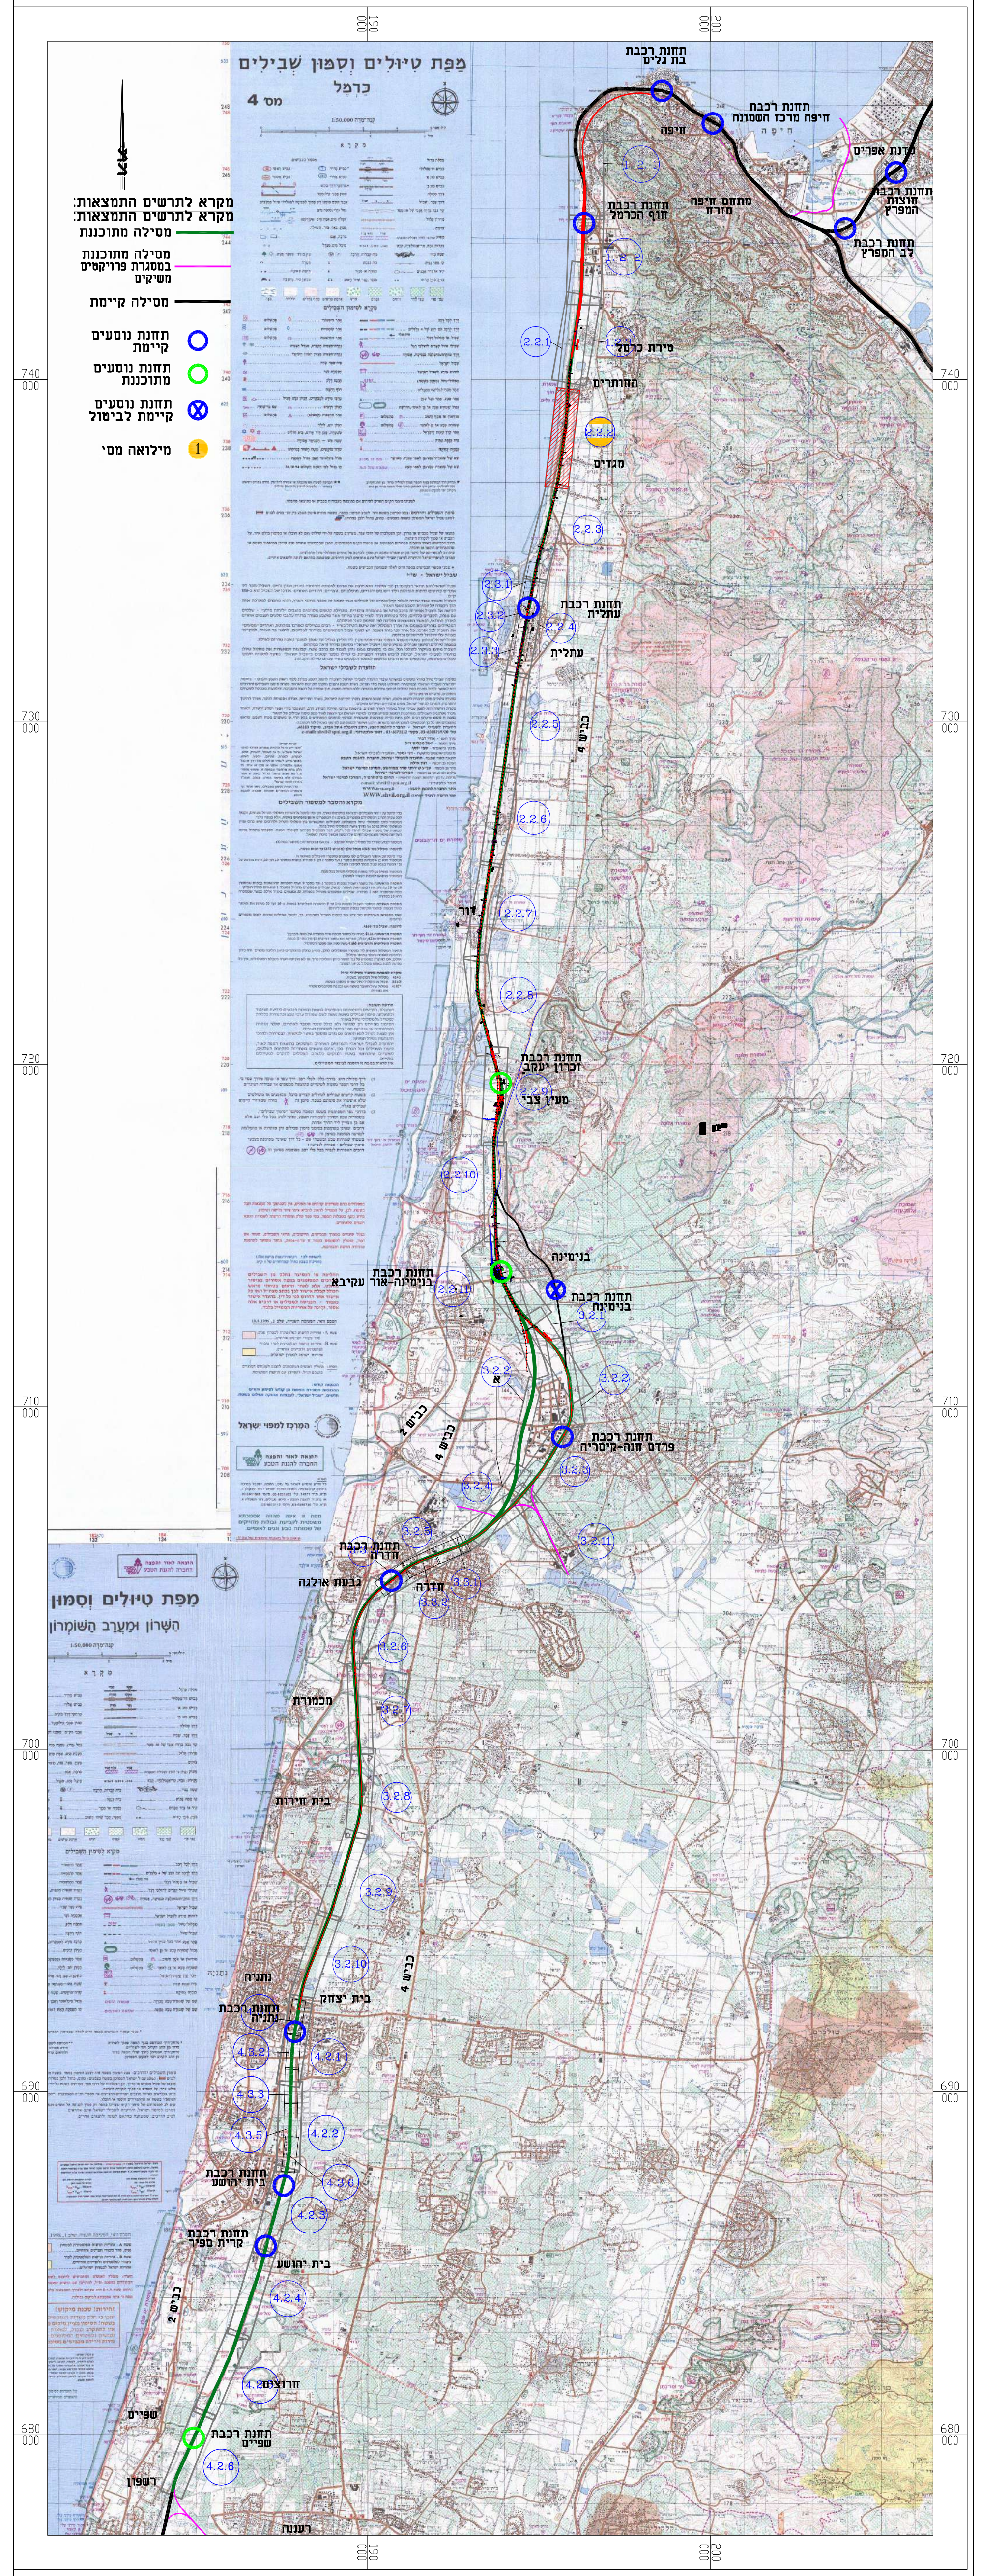
מַפַּת טִיּוּלִים וְסִמּוּן שְׁבִילִים
כַּרְמֶל
מס 4
תחנת רכבת בת גלים
תחנת רכבת חיפה מרכז השמונה
מַפַּת טִיּוּלִים וְסִמּוּן שְׁבִילִים
עֵמֶק חֶפֶר
תחנת רכבת
בנימינה
קיסריה
חדרה
נתניה

חוק התכנון והבניה, התשכ״ה – 1965
תכנית לתשתית לאומית

מסי תת״ל\65\א

שדרוג והרחבת מסילת החוף
בין תחנת חוף כרמל לשפיים

תנוחה ,ניקוז, חתך לאורך

גיליון 2.2.2 מק״מ 14+000 עד ק״מ 17+000

מחוז	חיפה, מרכז
מרחב תכנון מקומי	חיפה, חוף כרמל, מורדות הכרמל, ישובי הברון, עמק חפר, חוף השרון, נתניה, חדרה , פרדס חנה
רשות מקומית	חיפה, טירת הכרמל, חוף הכרמל, זיכרון יעקב, בנימינה - גבעת עדה, פרדס חנה - כרכור, חדרה, עמק חפר, נתניה, מנשה אלונה, חוף השרון, אור עקיבא ,ללא שיפוט
תוכנית בסמכות	ארצית
איחוד וחלוקה	ללא איחוד וחלוקה
הוראות לתכנון היתרים או הרשאות	תכנית שמכוחה ניתן להוציא היתרים או הרשאות
תאריך	31/1/2023
שלב	מתן תוקף
מהדורה	0
שטח התוכנית	דונם
קנה מידה	1:2500
מגיש התכנית	שם המגיש: חברת רכבת ישראל בע״מ חתימה:

חותמות מוסד התכנון :

חתימות

	שם	תפקיד	כתובת	טלפון	פקס	דוא״ל	שם	חתימה וחותמת
מדינת ישראל משרד הפנים הועדה הארצית לתכנון ולבנייה של תשתיות לאומיות								
בעלי קרקע מדינת ישראל ואחרים								
יזם התכנית רכבת ישראל משרד התחבורה באמצעות רכבת ישראל	יגאל קליימן	מנהל אגף תכנון	תחנת רכבת בת גלים ת.ד.8208 חיפה 31080	04-8564155	04-8564455	IGALK@rail.co.il	רכבת ישראל	
יזם התכנית רכבת ישראל משרד התחבורה באמצעות רכבת ישראל	תמי גנון	ממונה סטטוטוריקה ותכנון מוקדם	דרכי משה 3 לוד	03-7186247	08-6533517	tammyg@rail.co.il	רכבת ישראל	
מנהל הפרויקט: עסלעי הנדסה בע״מ O.SALI Engineering ltd.	עופר סלעי	מנהל הפרויקט	אלון התבור 20,קיסריה	04-6371711	04-6371712	ofer@sali.co.il	ע.סלע הנדסה בע״מ	
עורך התוכנית גרונר ד.א.ל מהנדסים בע״מ	גל גרונר	מתכנן ראשי	היוזמה 2 טירת הכרמל	04-8559111	04-8559100	haifa@grdel.co.il	גרונר ד.א.ל מהנדסים	
עורך התוכנית								
עורך התוכנית אמי-מתום מהנדסים ויועצים בע״מ AMY-METOM Engineers & Consultants Ltd.	אירנה ברודצקי	מתכנן	רח׳ יבנה 3, חיפה	04-8681111	04-8681112	ha-office@amymetom.co.il	אמי-מתום מהנדסים ויועצים בע״מ	
עורך התוכנית YENON RESEARCH & DESIGN LTD. ינון תכנון יעוץ ומחקר בע״מ	אלכס לרנר	מתכנן	היוזמה 10 טירת הכרמל	04-8569000	04-8569010	yenon@yenon.co.il	ינון	
אדריכלות נוף שלמה אהרונסון אדריכלים אדריכלות, אדריכלות נוף ותכנון ערים	ברברה אהרונסון	אדריכלית נוף	מבוא השער 4 עין כרם, ירושלים	02-6419143	02-6436825	aronson@aronson.co.il	שלמה אהרונסון אדריכלים	
אדריכלות Marcelo Fiszman Architects Ltd מרסלו פישמן אדריכלים בע״מ	מרסלו פישמן	מתכנן	רח׳ גרשון שץ 17 ת״א 6701753	077-5001067	077-3009127	office@mf-arch.co.il	מרסלו פישמן אדריכלים בע״מ	
אדריכלות נוף YENON RESEARCH & DESIGN LTD. ינון תכנון יעוץ ומחקר בע״מ	סמדר כהן	אדריכלית נוף	היוזמה 10 טירת הכרמל	04-8569000	04-8569010	yenon@yenon.co.il	ינון	
מודד מוסמך חץ הצפון מיפוי והנדסה בע״מ	סביון שחם	מודד מוסמך	היוזמה 2 טירת הכרמל	04-8580355	04-8580377	office@hetz-hazafon.co.il	חץ הצפון	

P:\6279-2\DD-FT\SP\tnaei-saf-2\2-2-X.dwg, 22/05/2023 11:49:04, DesignJet 750C Plus C4709B.pc3