מינהל התכנון

הועדה הארצית לתכנון ובניה של תשתיות לאומיות

חוק התכנון והבניה, התשכ"ה

תכנית לתשתית לאומית מס תתל/ 65/ א

המאושרות ע"י הממשלה לפי החלטה תמאמ/ 4

מיום 20.12.2023

וחתומה בידי מזכיר ממשלה ובידי מזכיר הועדה

אפרת

מזכיר ממשלה
תאריך:

מזכיר הועדה
תאריך: 20/12/2023

תכנית תתל/ 65/ א 14/08/2023

תנוחה ע״ר מצב קיים

קנ״מ 1:2500

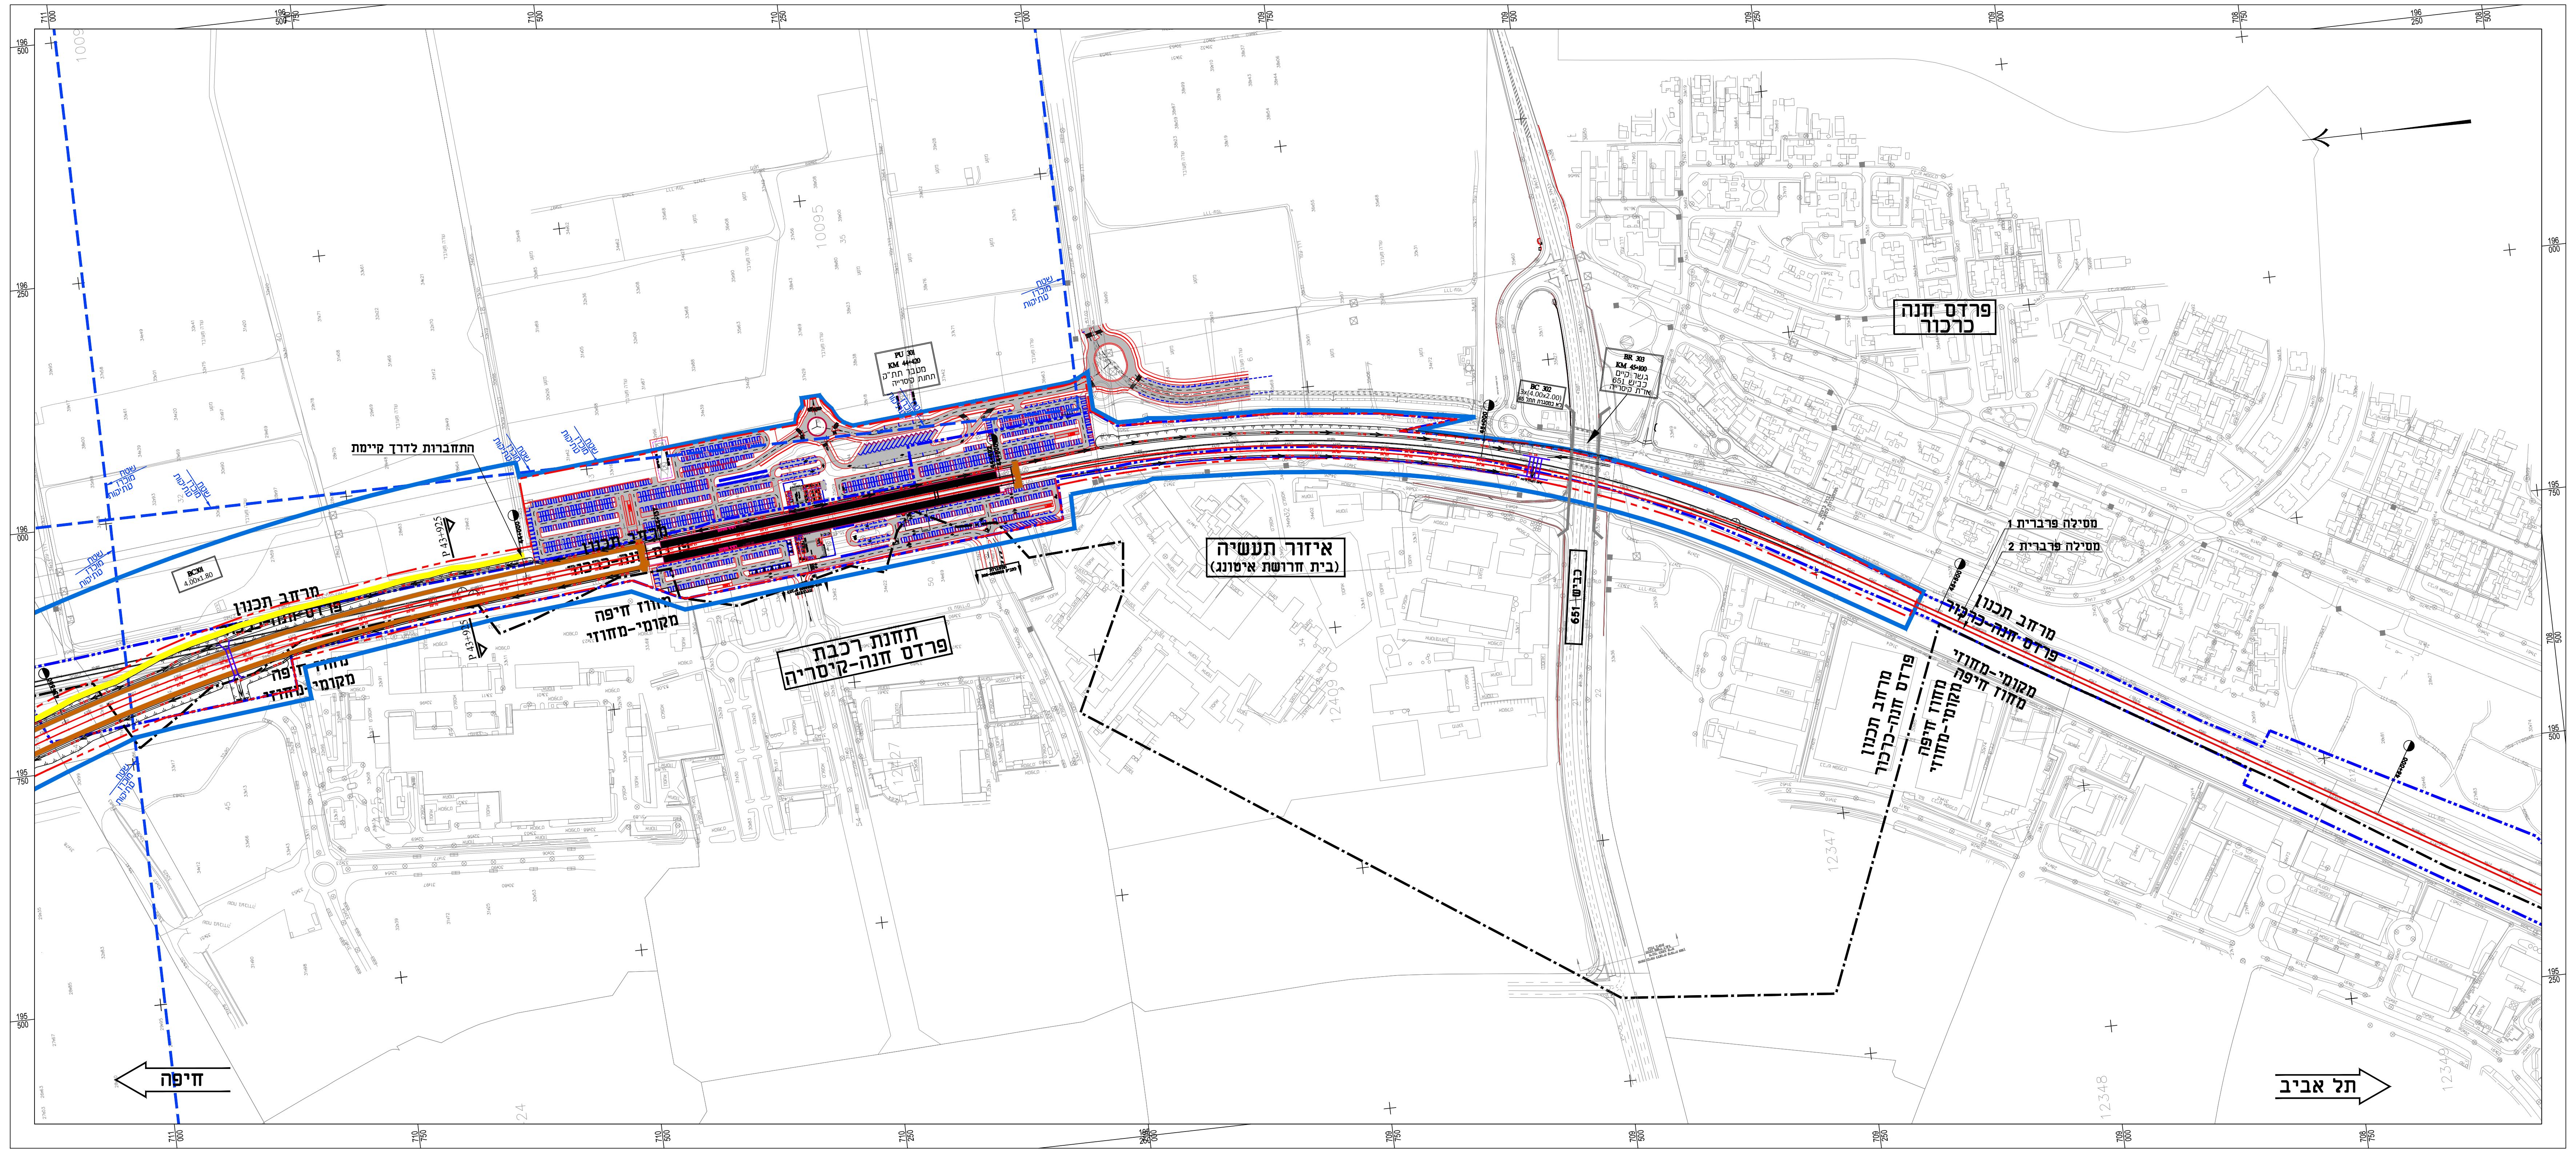

חתך לאורך מסילות פרבריות

קנ״מ 1:250\2500

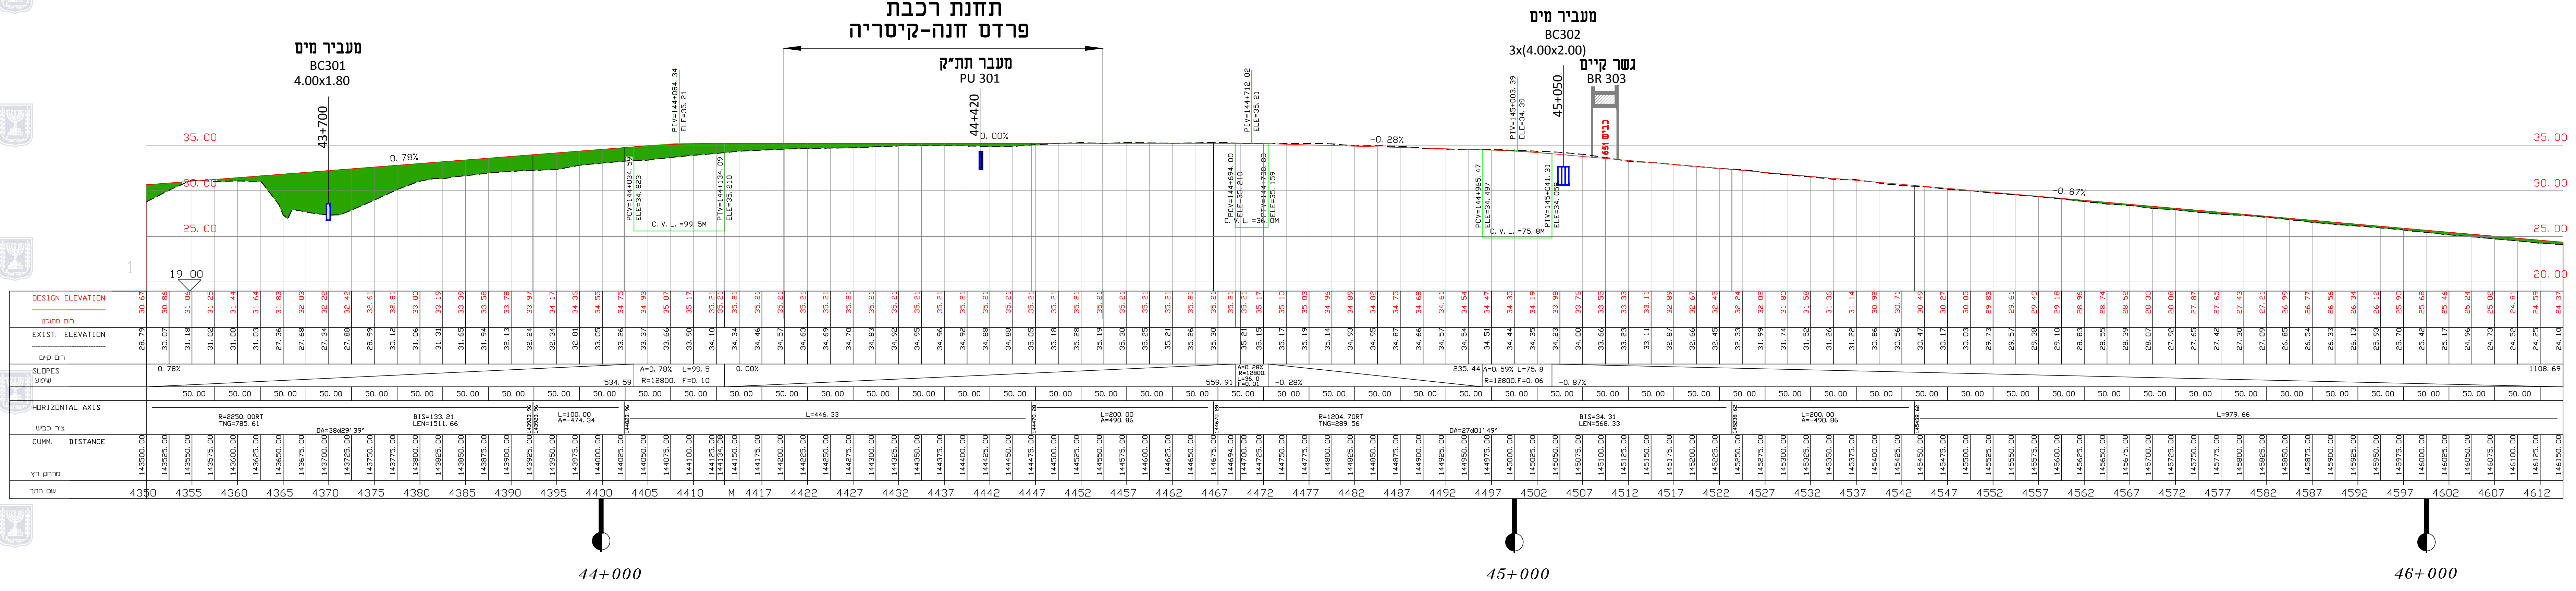

מקרא

- גבול תכנית
- גבול רצועת רכבת מוצע
- גבול רצועת רכבת קיים
- גבול שטח שיפוט
- ציר מסילה מתוכננת
- ציר מסילה קיים
- מסילה מתוכננת בפרויקט משיק
- מסילה ננטשת
- 20+000 קילומטר מסילה/ חתך
- תחנת נוסעים מוצעת-מבנה/רציפים
- גשר רכבת
- גשר כביש
- מנהרת רכבת/רכב
- מעבר תחתי
- עתיקות
- כיווני זרימה בתעלת ניקוז
- מעביר מים מתוכנן
- מבנה שליטה ובקרה קיים- שו״ב
- מבנה שליטה ובקרה מתוכנן- שו״ב
- מבנה תחנת השנאה תת״ל 18 - תה״ר
- מבנה חישמול מתוכנן
- שטח התארגנות
- קיר מתוכנן
- קיר אקוסטי קיים
- קיר אקוסטי מתוכנן
- גדר מתוכננת
- מפלג
- דרך קיימת
- דרך מתוכננת
- דרך שירות
- דרך חקלאית
- גבול גוש ומספרו
- גבול חלקה ומספרה
- מספר הדרך
- קווי בנין
- רוחב הדרך
- גבול תכנון (גבול תכנון; ק״מ 3+508; ק״מ 3+557)

חתך לאורך

- מסילה מתוכננת
- רום קרקע קיימת
- 🟧 חפירה
- 🟩 מילוי

תרשים סביבה

קנ״מ 1:100000

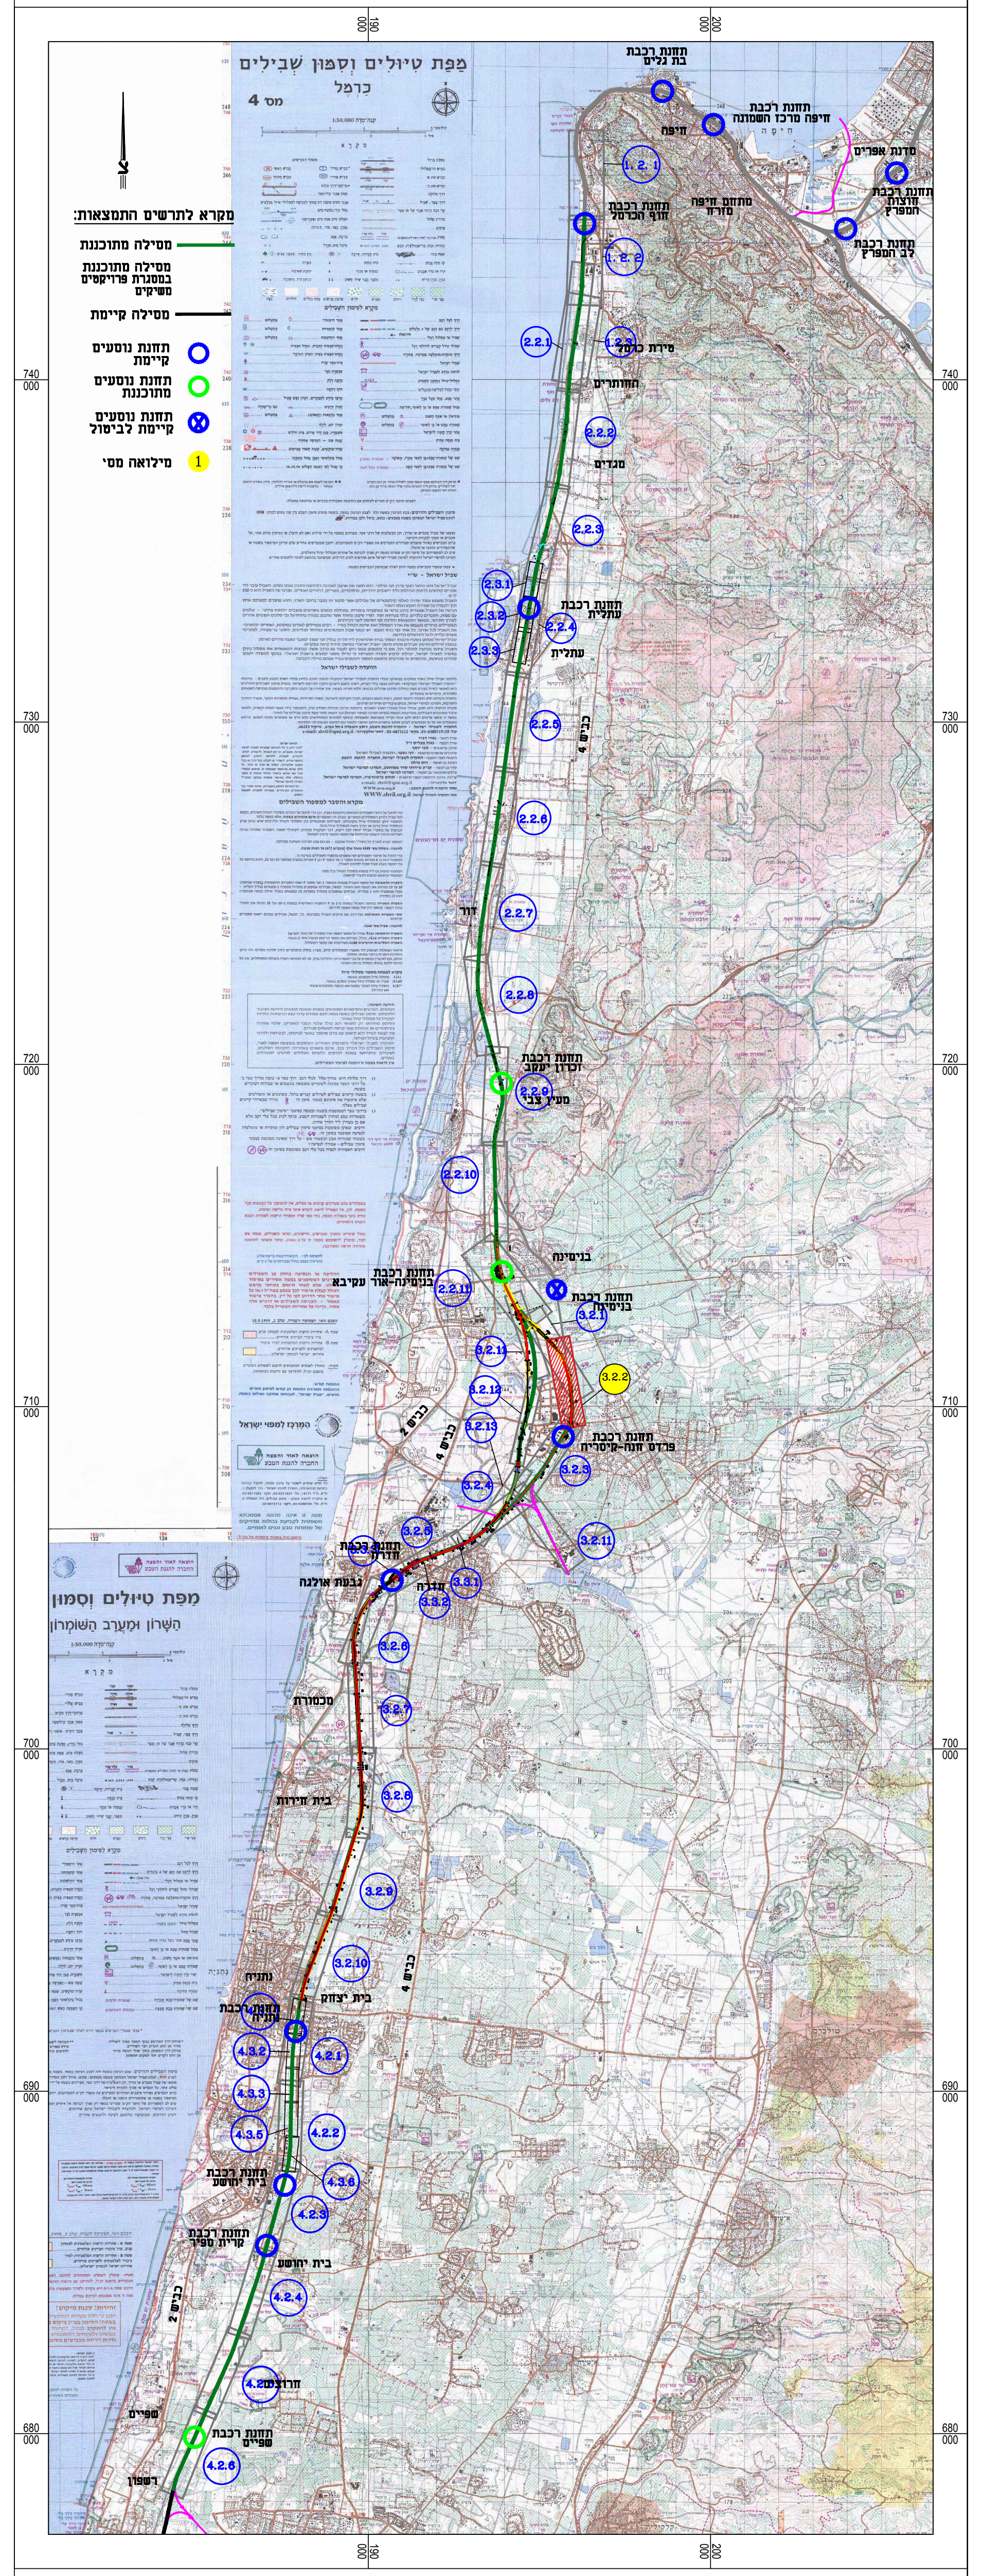

חוק התכנון והבניה, התשכ״ה - 1965

תכנית לתשתית לאומית

מסי תת״ל/65/א׳

שדרוג והרחבת מסילות החוף בין תחנת חוף הכרמל לשפיים

תנוחה, ניקוז וחתך לאורך

גיליון 3.2.2 (ק״מ 43+500-46+150)

מחוז	חיפה, מרכז
מרחב תכנון מקומי	חיפה, חוף כרמל, מורדות הכרמל, ישובי הברון, עמק חפר, חוף השרון, נתניה, חדרה, פרדס חנה
רשות מקומית	חיפה, טירת הכרמל, חוף הכרמל, זיכרון יעקב, בנימינה - גבעת עדה, פרדס חנה - כרכור, חדרה, עמק חפר, נתניה, מנשה אלונה, חוף השרון, אור עקיבא, ללא שיפוט
תוכנית בסמכות	ארצית
איחוד וחלוקה	ללא איחוד וחלוקה
הוראות לתכנון היתרים או הרשאות	תכנית שמכוחה ניתן להוציא היתרים או הרשאות
תאריך	31/01/2023
שלב	מתן תוקף
מהדורה	0
שטח התוכנית	דונם
קנה מידה	1:2500
מגיש התכנית – שם המגיש	חברת רכבת ישראל בע״מ
חתימה:	

חותמות מוסד התכנון :

חתימות

מדינת ישראל
משרד הפנים
הועדה הארצית לתכנון ולבנייה של תשתיות לאומיות
חתימה וחותמת

בעלי קרקע: **מדינת ישראל ואחרים**
חתימה וחותמת

יזם התכנית: משרד התחבורה באמצעות רכבת ישראל
חתימה וחותמת
שם: יגאל קליימן | תפקיד: מנהל אגף תכנון | כתובת: תחנת רכבת בת גלים ת.ד 8208 חיפה 31080
טלפון: 04-8564155 | פקס: 04-8564455 | דוא״ל: IGALK@rail.co.il | שם: רכבת ישראל

יזם התכנית: משרד התחבורה באמצעות רכבת ישראל
חתימה וחותמת
שם: תמי גנון | תפקיד: ממונה סטטוטוריקה ותכנון מוקדם | כתובת: דרכי משה 3 לוד
טלפון: 03-7186247 | פקס: 03-7186255 | דוא״ל: tammyg@rail.co.il | שם: רכבת ישראל

מנהל הפרויקט: ע.סלעי הנדסה בע״מ O.SALI Engineering ltd.
חתימה וחותמת
שם: עופר סלעי | תפקיד: מנהל הפרויקט | כתובת: אלון התבור 20, קיסריה
טלפון: 04-6371711 | פקס: 04-6371712 | דוא״ל: ofer@sali.co.il | שם: ע.סלע הנדסה בע״מ

עורך התוכנית: גרונר ד.א.ל מהנדסים בע״מ
חתימה וחותמת
שם: גל גרונר | תפקיד: מתכנן ראשי | כתובת: היוזמה 2 טירת הכרמל
טלפון: 04-8559111 | פקס: 04-8559100 | דוא״ל: haifa@grdel.co.il | שם: גרונר ד.א.ל מהנדסים

עורך התוכנית
חתימה וחותמת
שם: | תפקיד: | כתובת:
טלפון: | פקס: | דוא״ל: | שם:

עורך התוכנית: אמי-מתום מהנדסים ויועצים בע״מ AMY-METOM Engineers & Consultants Ltd.
חתימה וחותמת
שם: אירינה ברודצקי | תפקיד: מתכנן | כתובת: רח׳ יבנה 3, חיפה
טלפון: 04-8681111 | פקס: 04-8681112 | דוא״ל: ha-office@amymetom.co.il | שם: אמי-מתום מהנדסים ויועצים בע״מ

עורך התוכנית: ינון תכנון יעוץ ומחקר בע״מ
חתימה וחותמת
שם: אלכס לרנר | תפקיד: מתכנן | כתובת: היוזמה 10 טירת הכרמל
טלפון: 04-8569000 | פקס: 04-8569010 | דוא״ל: yenon@yenon.co.il | שם: ינון

אדריכלות נוף: שלמה אהרונסון אדריכלים – אדריכלות, אדריכלות נוף ותכנון ערים
חתימה וחותמת
שם: ברברה אהרונסון | תפקיד: אדריכלית נוף | כתובת: מבוא השער 4 עין כרם, ירושלים
טלפון: 02-6419143 | פקס: 02-6436825 | דוא״ל: aronson@aronson.co.il | שם: שלמה אהרונסון אדריכלים

אדריכלות: מרסלו פישמן אדריכלים בע״מ Marcelo Fiszman Architects Ltd
חתימה וחותמת
שם: מרסלו פישמן | תפקיד: מתכנן | כתובת: רח׳ גרשון שץ 17 ת״א 6701753
טלפון: 077-5001067 | פקס: 077-3009127 | דוא״ל: office@mf-arch.co.il | שם: מרסלו פישמן אדריכלים בע״מ

אדריכלות נוף: ינון תכנון יעוץ ומחקר בע״מ
חתימה וחותמת
שם: סמדר כהן | תפקיד: אדריכלית נוף | כתובת: היוזמה 10 טירת הכרמל
טלפון: 04-8569000 | פקס: 04-8569010 | דוא״ל: yenon@yenon.co.il | שם: ינון

מודד מוסמך: חץ הצפון
חתימה וחותמת
שם: סביון שחם | תפקיד: מודד מוסמך | כתובת: היוזמה 2 טירת הכרמל
טלפון: 04-8580355 | פקס: 04-8580377 | דוא״ל: office@hetz-hazafon.co.il | שם: חץ הצפון