


תנוחה עייר מצב קיים

1:1000 מ"מ

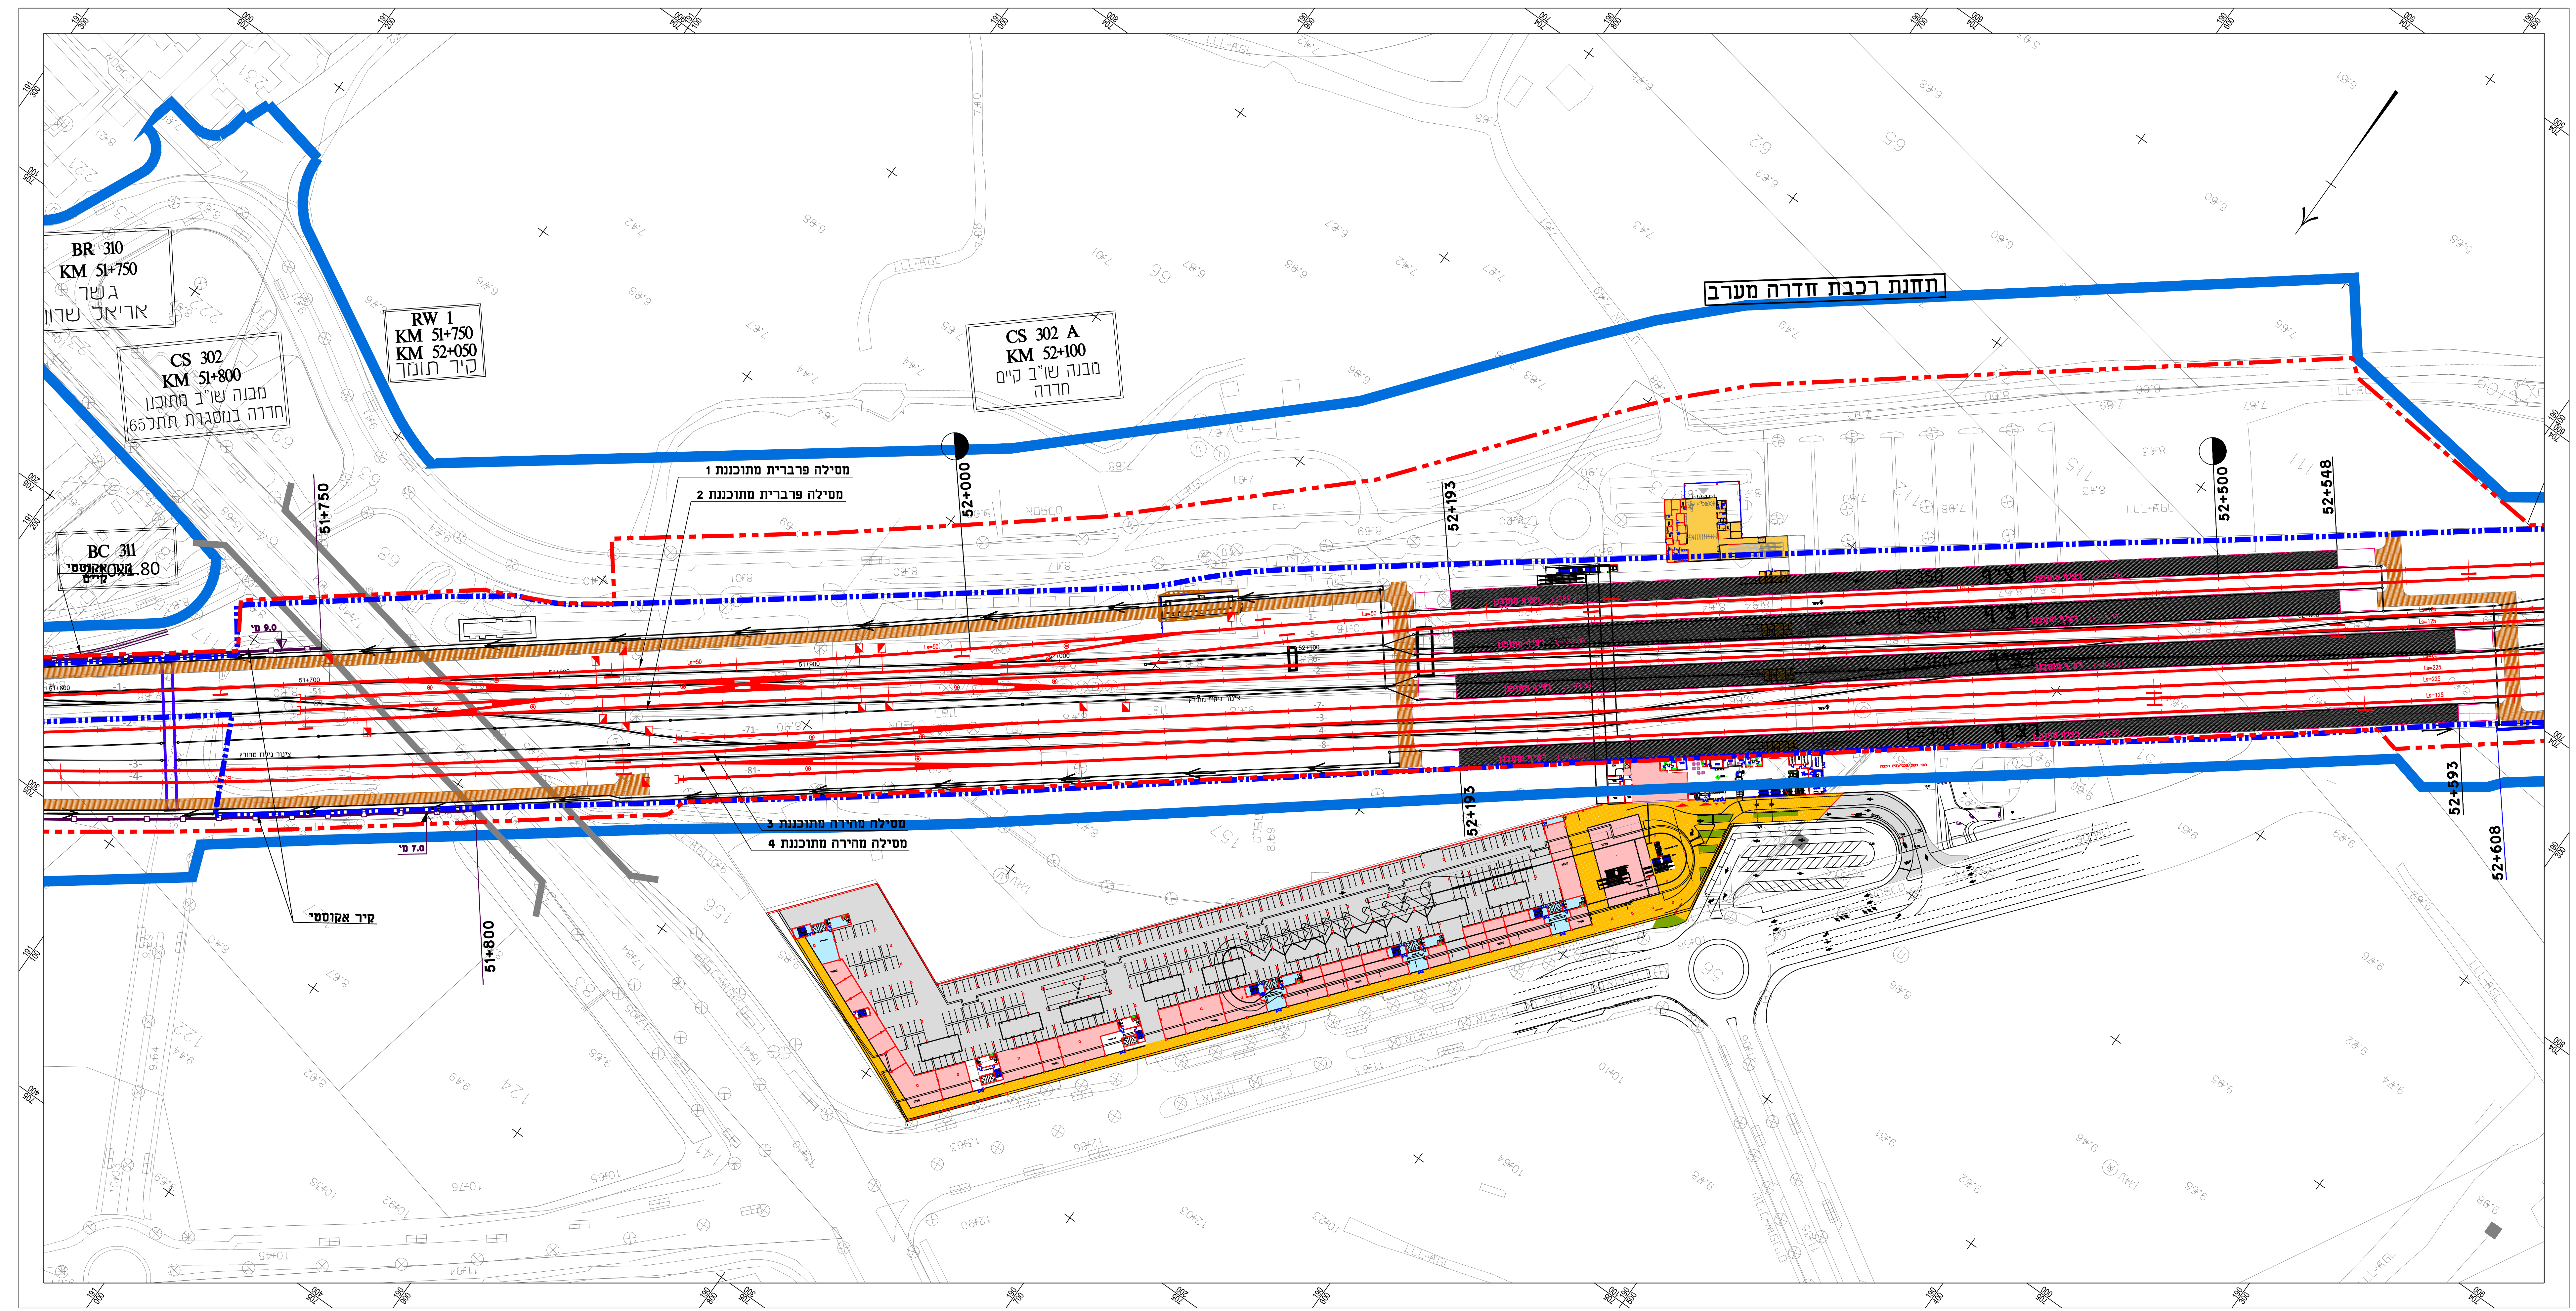


**תחנת רכבת חדרה
רציפים**

גשר עילי לה"ר

PO303


חתך לאורך מסילות פרבריות

קניימ 1:100\1000

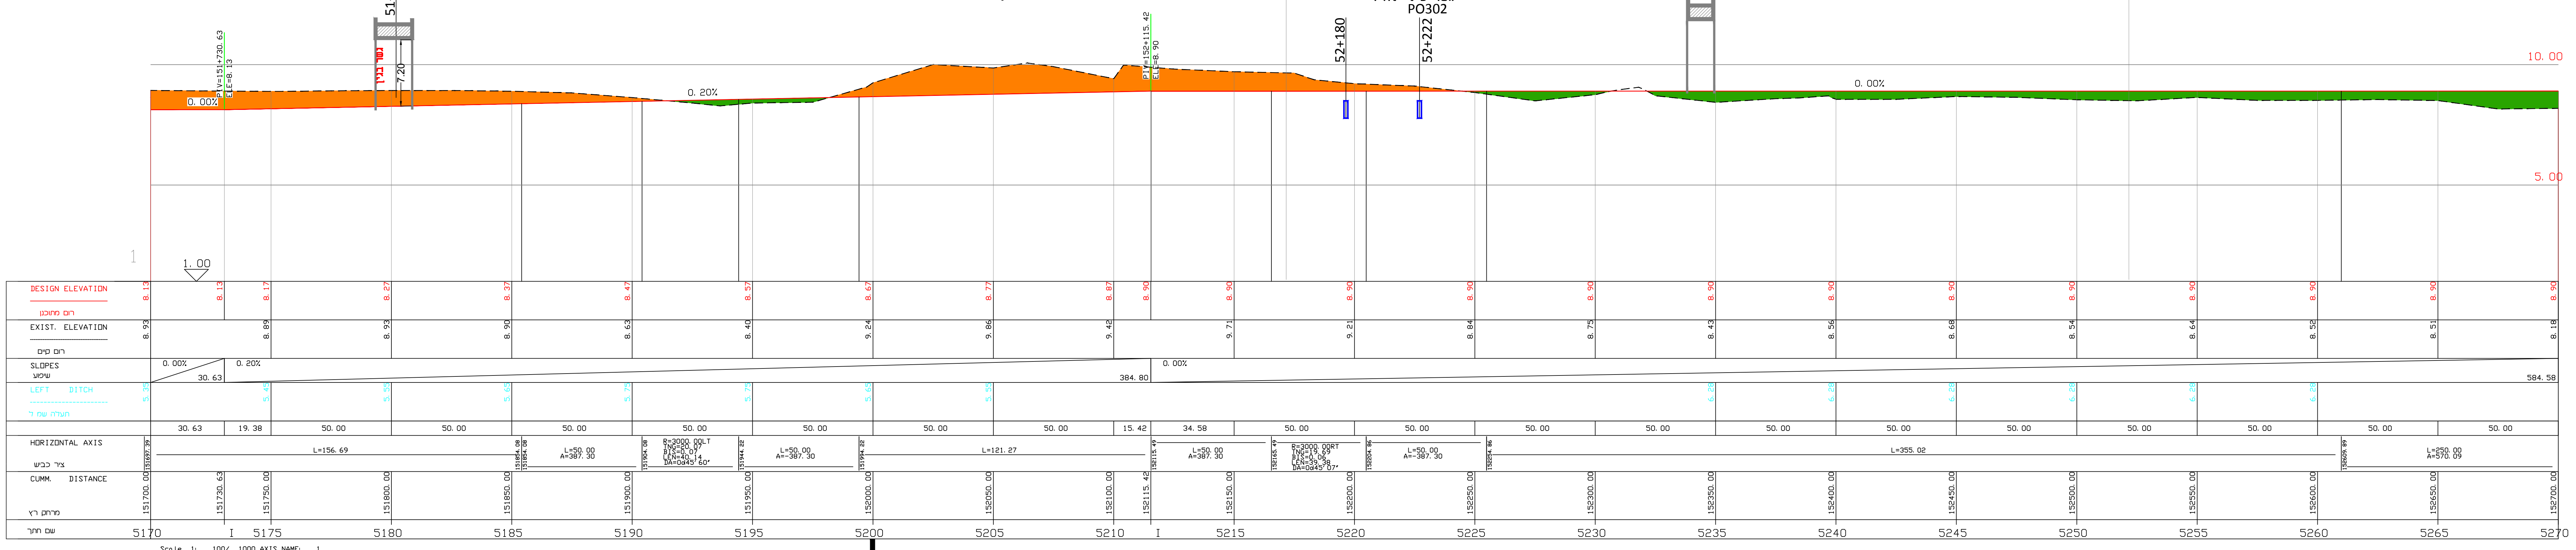

52+000

מקרא

- ורכבת מוצע
ורכבת קיים
שישים
ותומנות
קיים
תנות פרויקט משק
ת
ת/זל: חתך
מוצעת-מבנה/רצפים
ת/רכב
ת/בשת ניסוח
ת/חוכן
ורכבת קיים- שריב
ת/בשת ת/חוכן- שריב
ת/שואה ת/חז' 18 - תהדר
זל ת/חוכן
תנות
קיים
ת/חוכן
ת
ת
ספרי
ומספרה
ת/חוכן

חתך לאורך


-

חתך לאורך

-

תרשים סביבה
דיון 4400000

1.1000000 1.1000000

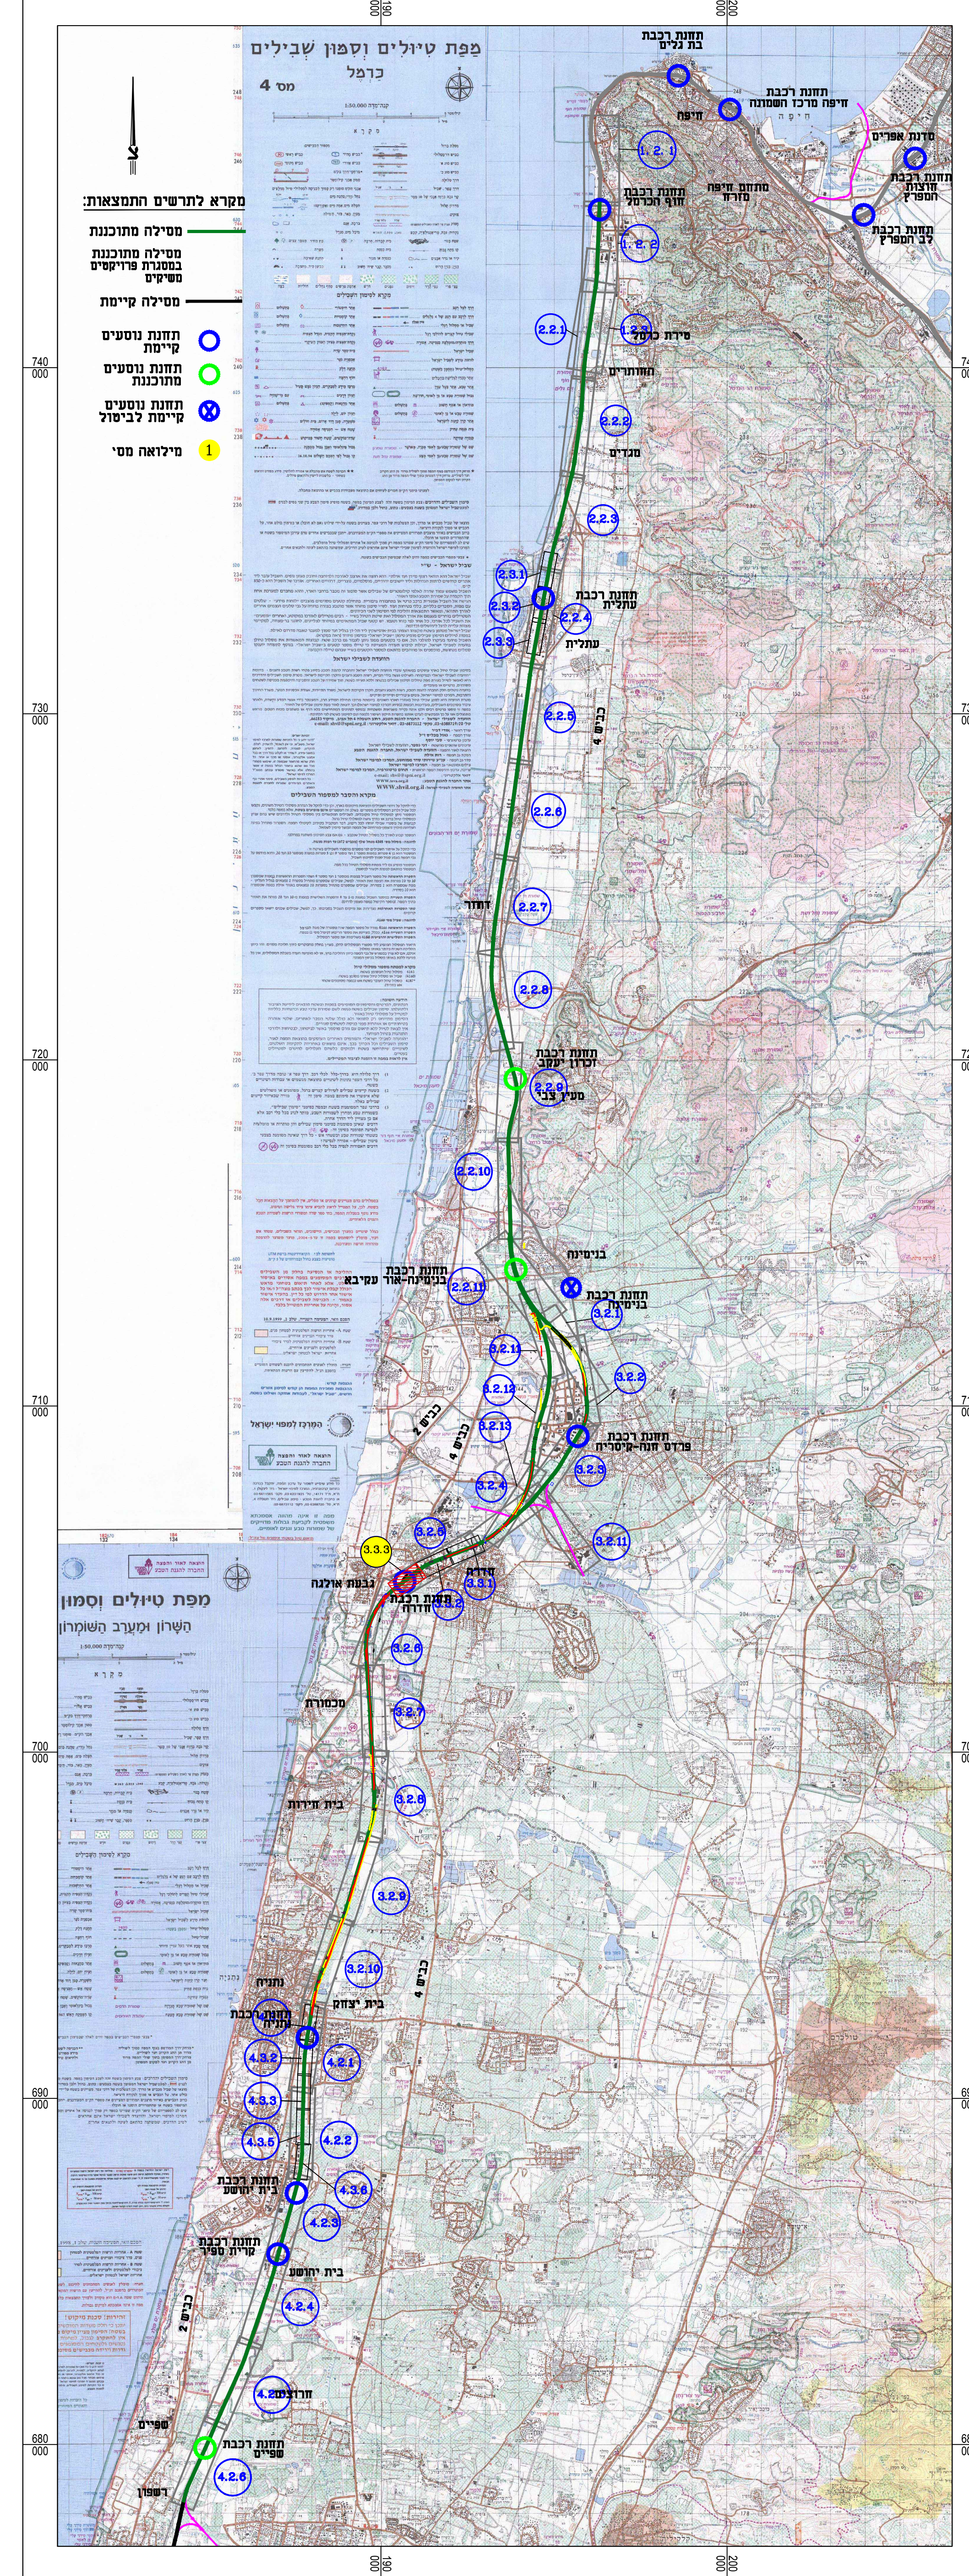

תימות

[illegible]