

חוק התכנון והבניה"ה-1965
הועדה הארצית לתכנון ולבניה של תשתיות לאומיות

תת"ל 33

מסילה רביעית באילון

קטע ת"א מרכז-לוד

תכנית לחשתית לאומית


חנתן לאורך ותנוחה

גליון מס' 2 מתוך 4
קנ"מ : 5,000 : 1 : 500


מחוז: תל אביב,מרכז
מרחבי תכנון מקומיים:

- ועדה מקומית תל אביב-יפו
- ועדה מקומית רמת גן
- ועדה מקומית גבעתיים
- מרחב תכנון מחוזי-מקומי (מחוז ת"א)
- ועדה מרחבית אור יהודה-אזור
- ועדה מרחבית מצפה אפק
- ועדה מקומית עמק לוד
- ועדה מקומית לוד

דו"תמת מוסד התכנון :




 


שלב: אישר תכנית : מהדורה: 14 : תאריך: 25.04.2018

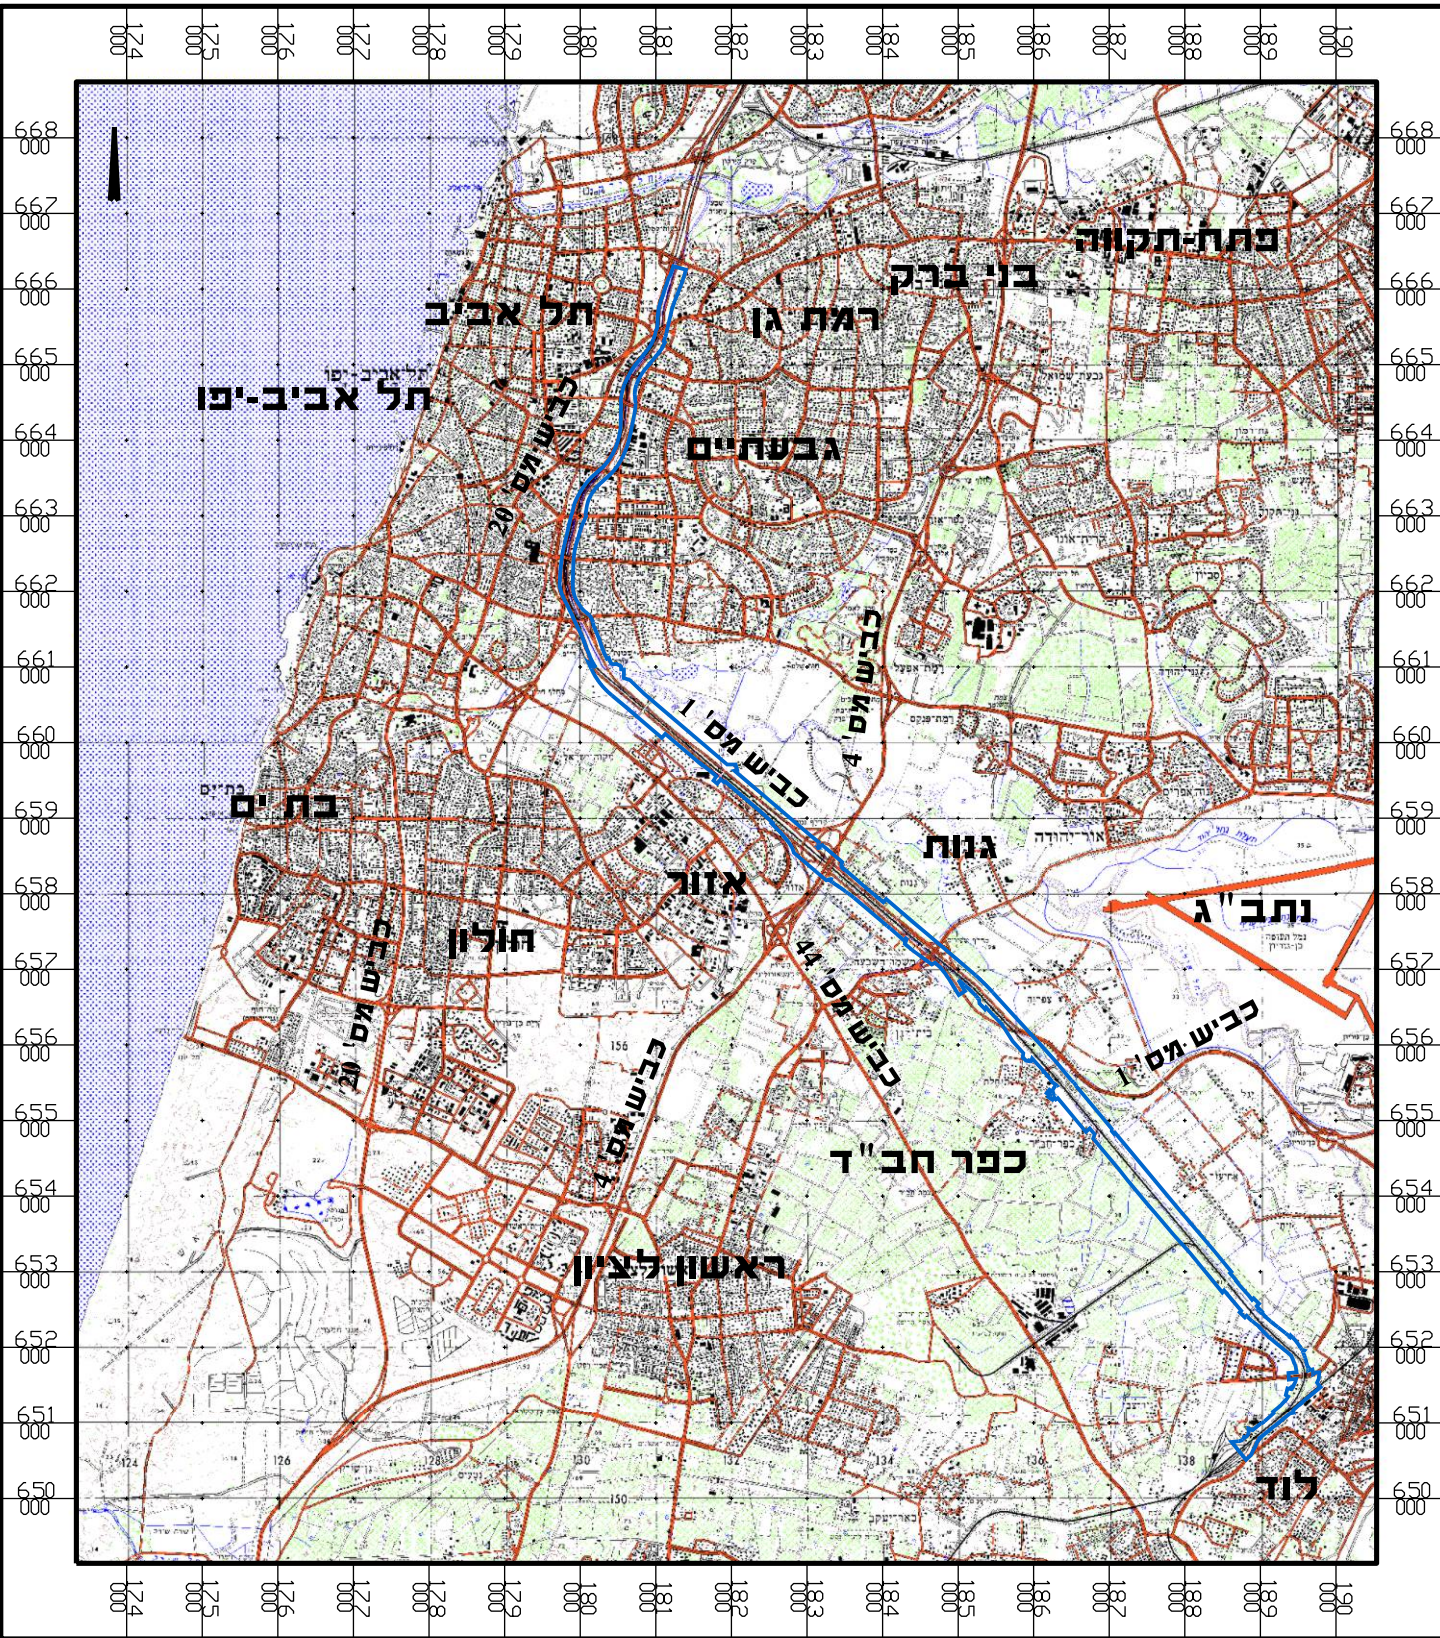

מפת מפתח:

קנ"מ : 100 : 000 : 1

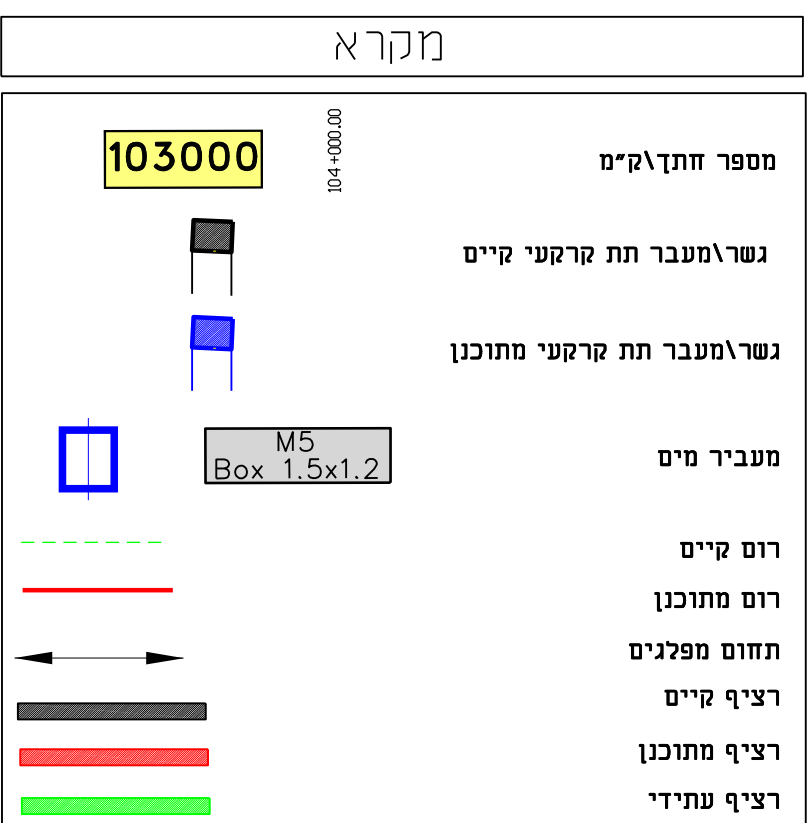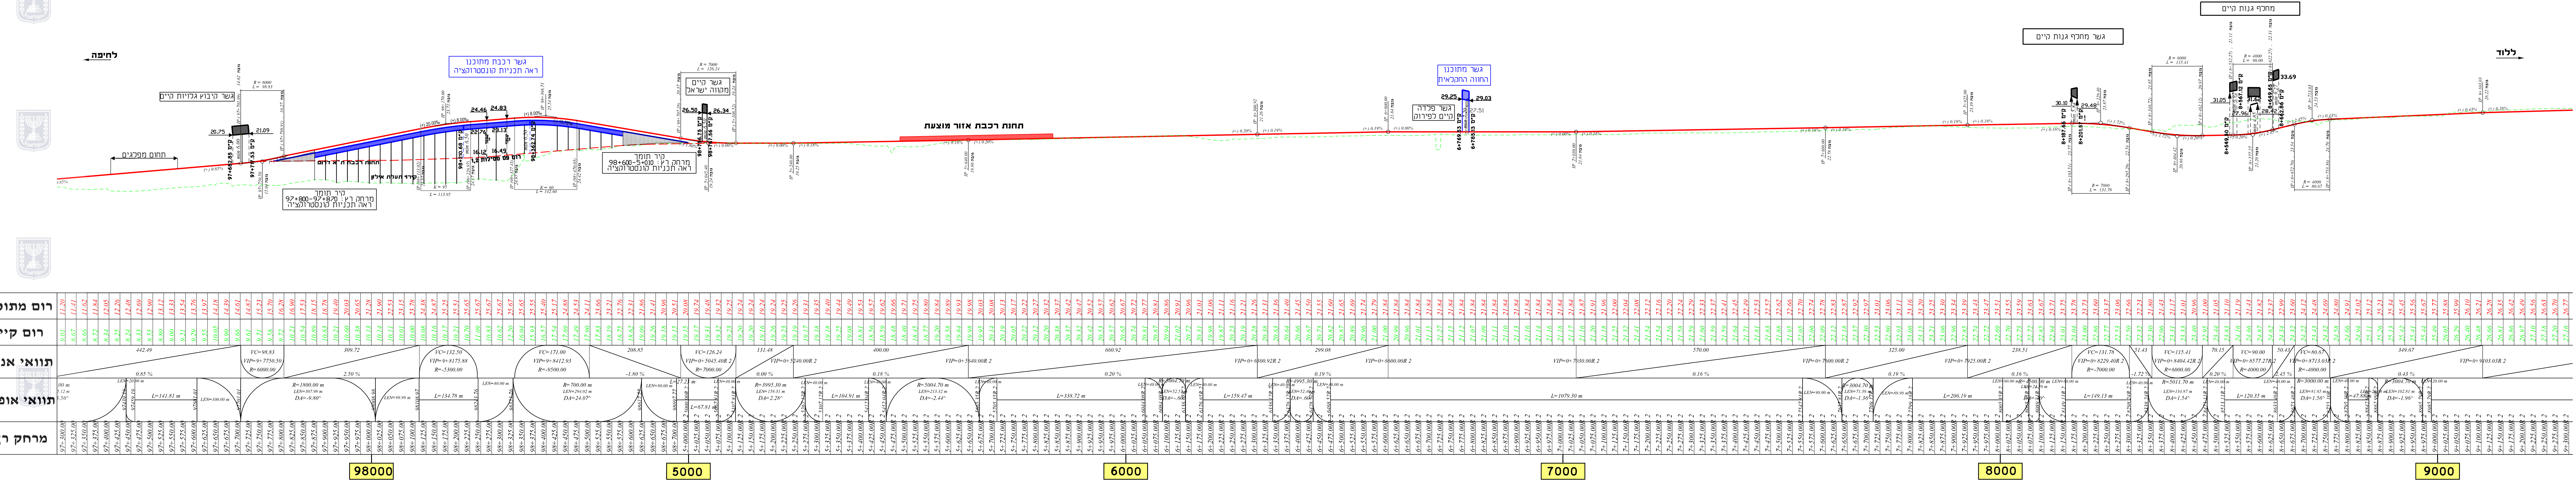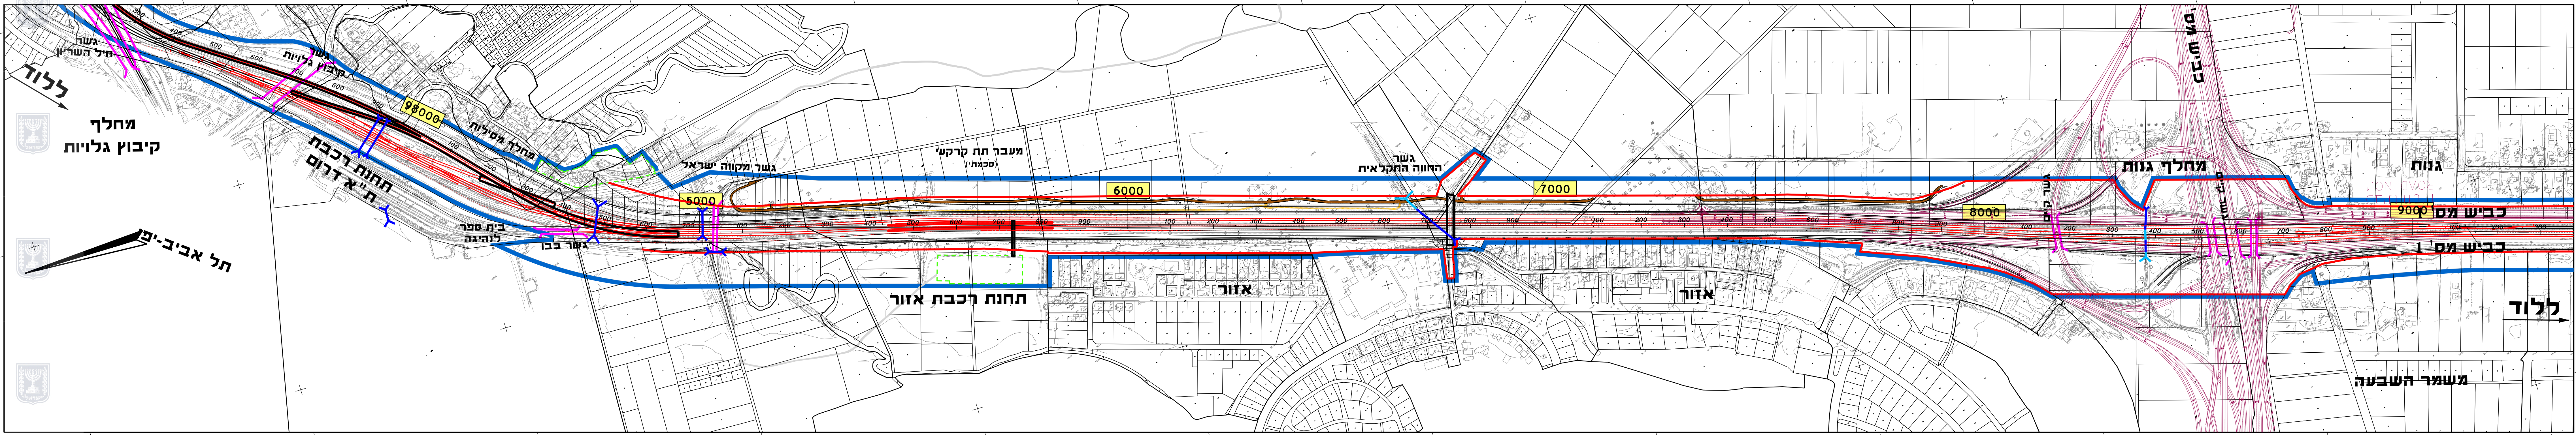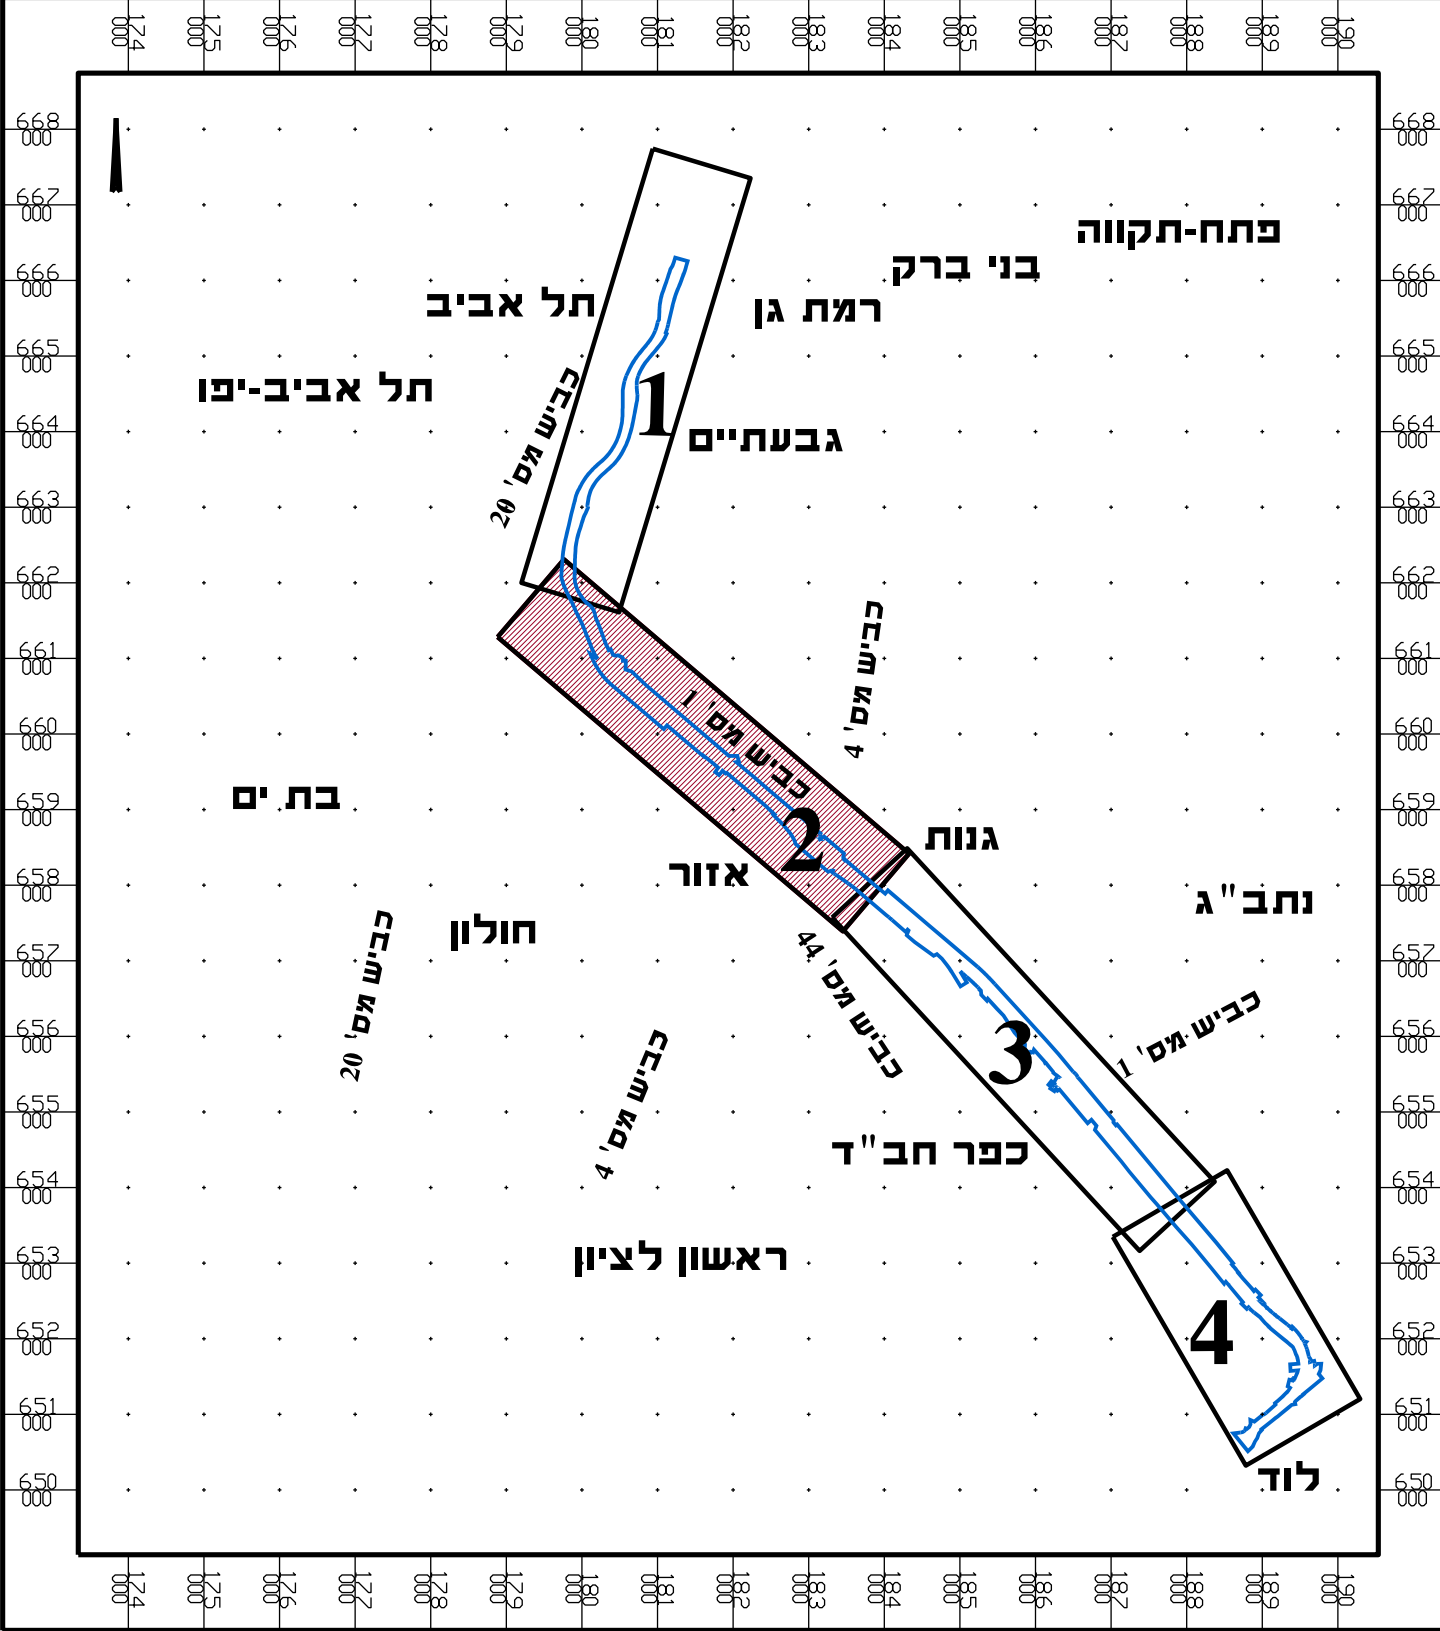

ברוך שטיין (בא) כי מידת הפקת הטעמים/העניינים מהאזור והתכנון זו, שהגיע יד כיים,
ויש להבהיר מידת הפקת הטעמים מהאזור והתכנון וההחלטות שהתקבלו.
דיווח והחלטות הוועדה: מידת הפקת הטעמים מהאזור והתכנון וההחלטות שהתקבלו.
(נכדל ודו"ת הוועדה)

שם המודד: _____ מספר רישון: _____ רחוקה: _____ חשד: _____