חוק התכנון והבנייה, התשכ"ה- 1965
הועדה הארצית לתכנון ולבניה של תשתיות לאומיות

תת״ל 33
מסילה רביעית באיילון
קטע ת״א מרכז-לוד

תכנית לתשתית לאומית

חתך לאורך ותנוחה
גליון מסי 4 מתוך 4
קנ״מ : 1 : 5,000 \ 1 : 500

מחוז: תל אביב,מרכז

מרחבי תכנון מקומיים:
- ועדה מקומית תל אביב-יפו
- ועדה מקומית רמת גן
- ועדה מקומית גבעתיים
- מרחב תכנון מחוזי-מקומי (מחוז ת״א)
- ועדה מרחבית אור יהודה-אזור
- ועדה מרחבית מצפה אפק
- ועדה מקומית עמק לוד
- ועדה מקומית לוד

חותמת מוסד התכנון :

שלב: אישור תכנית מהדורה: 14 תאריך: 25.04.2018

תרשים סביבה :
קנ״מ 1 : 100 000

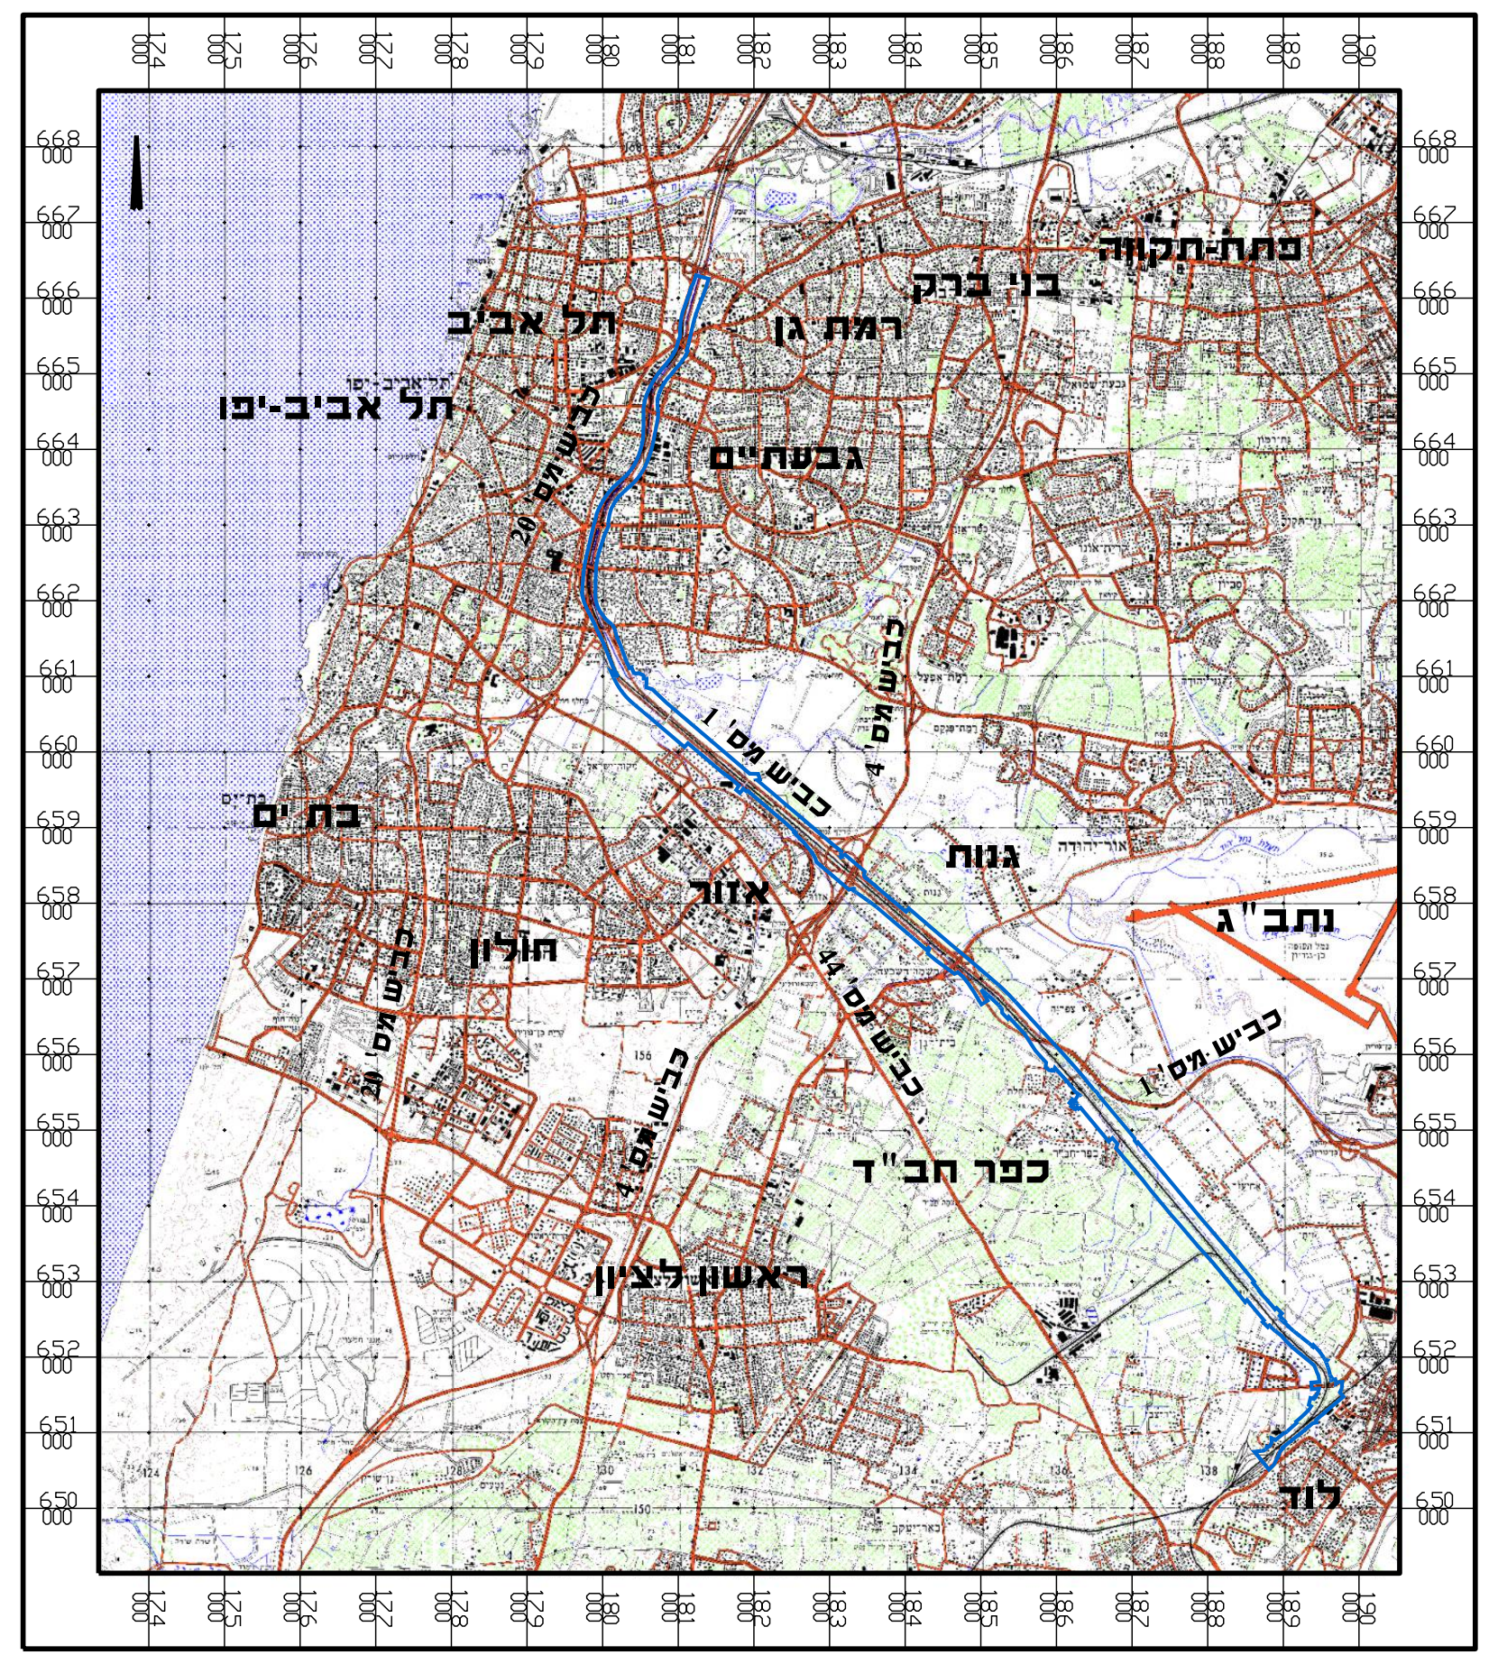

מפת מפתח:
קנ״מ 1 : 100 000

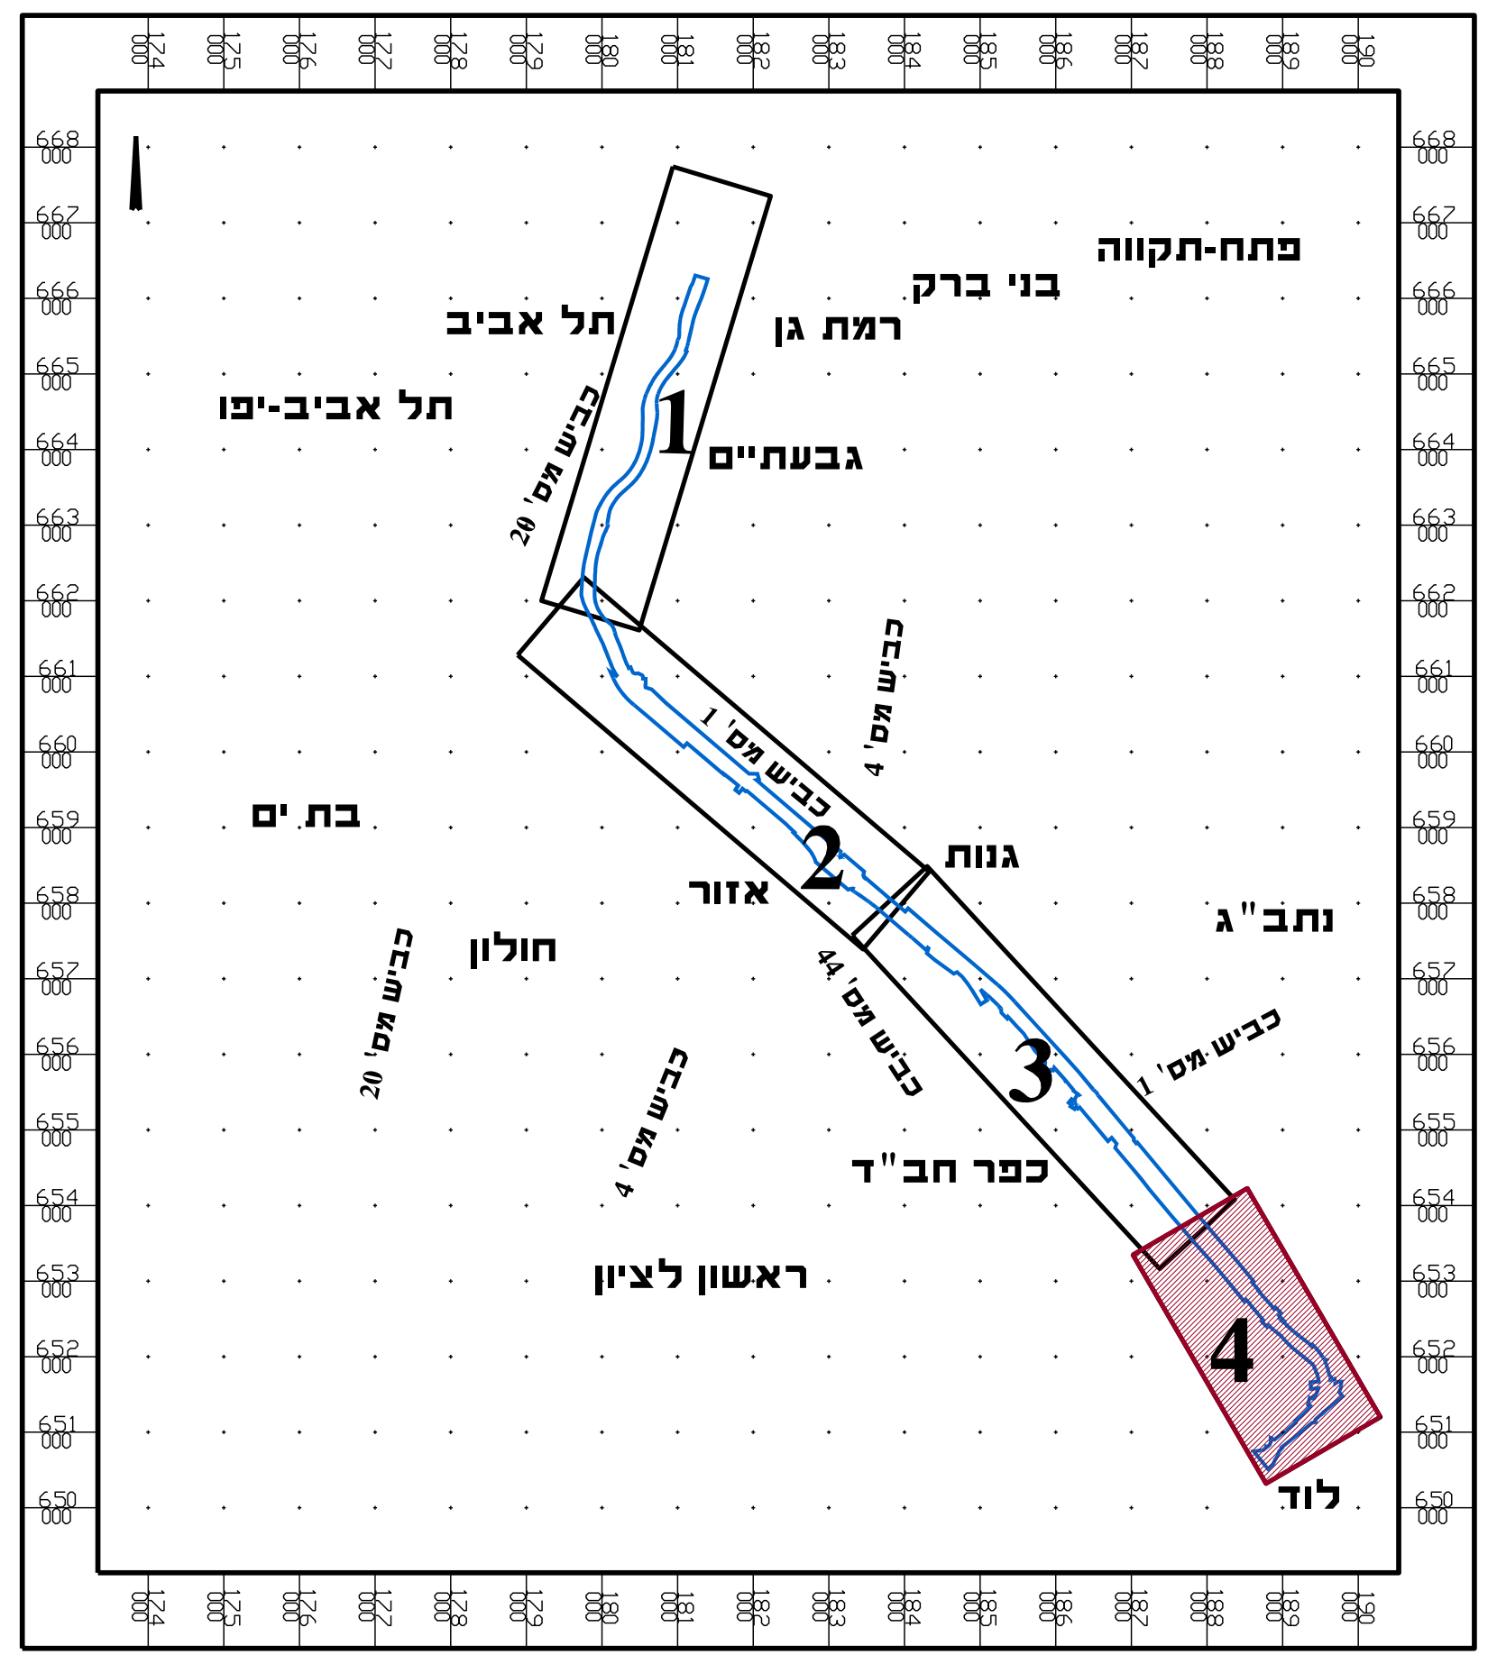

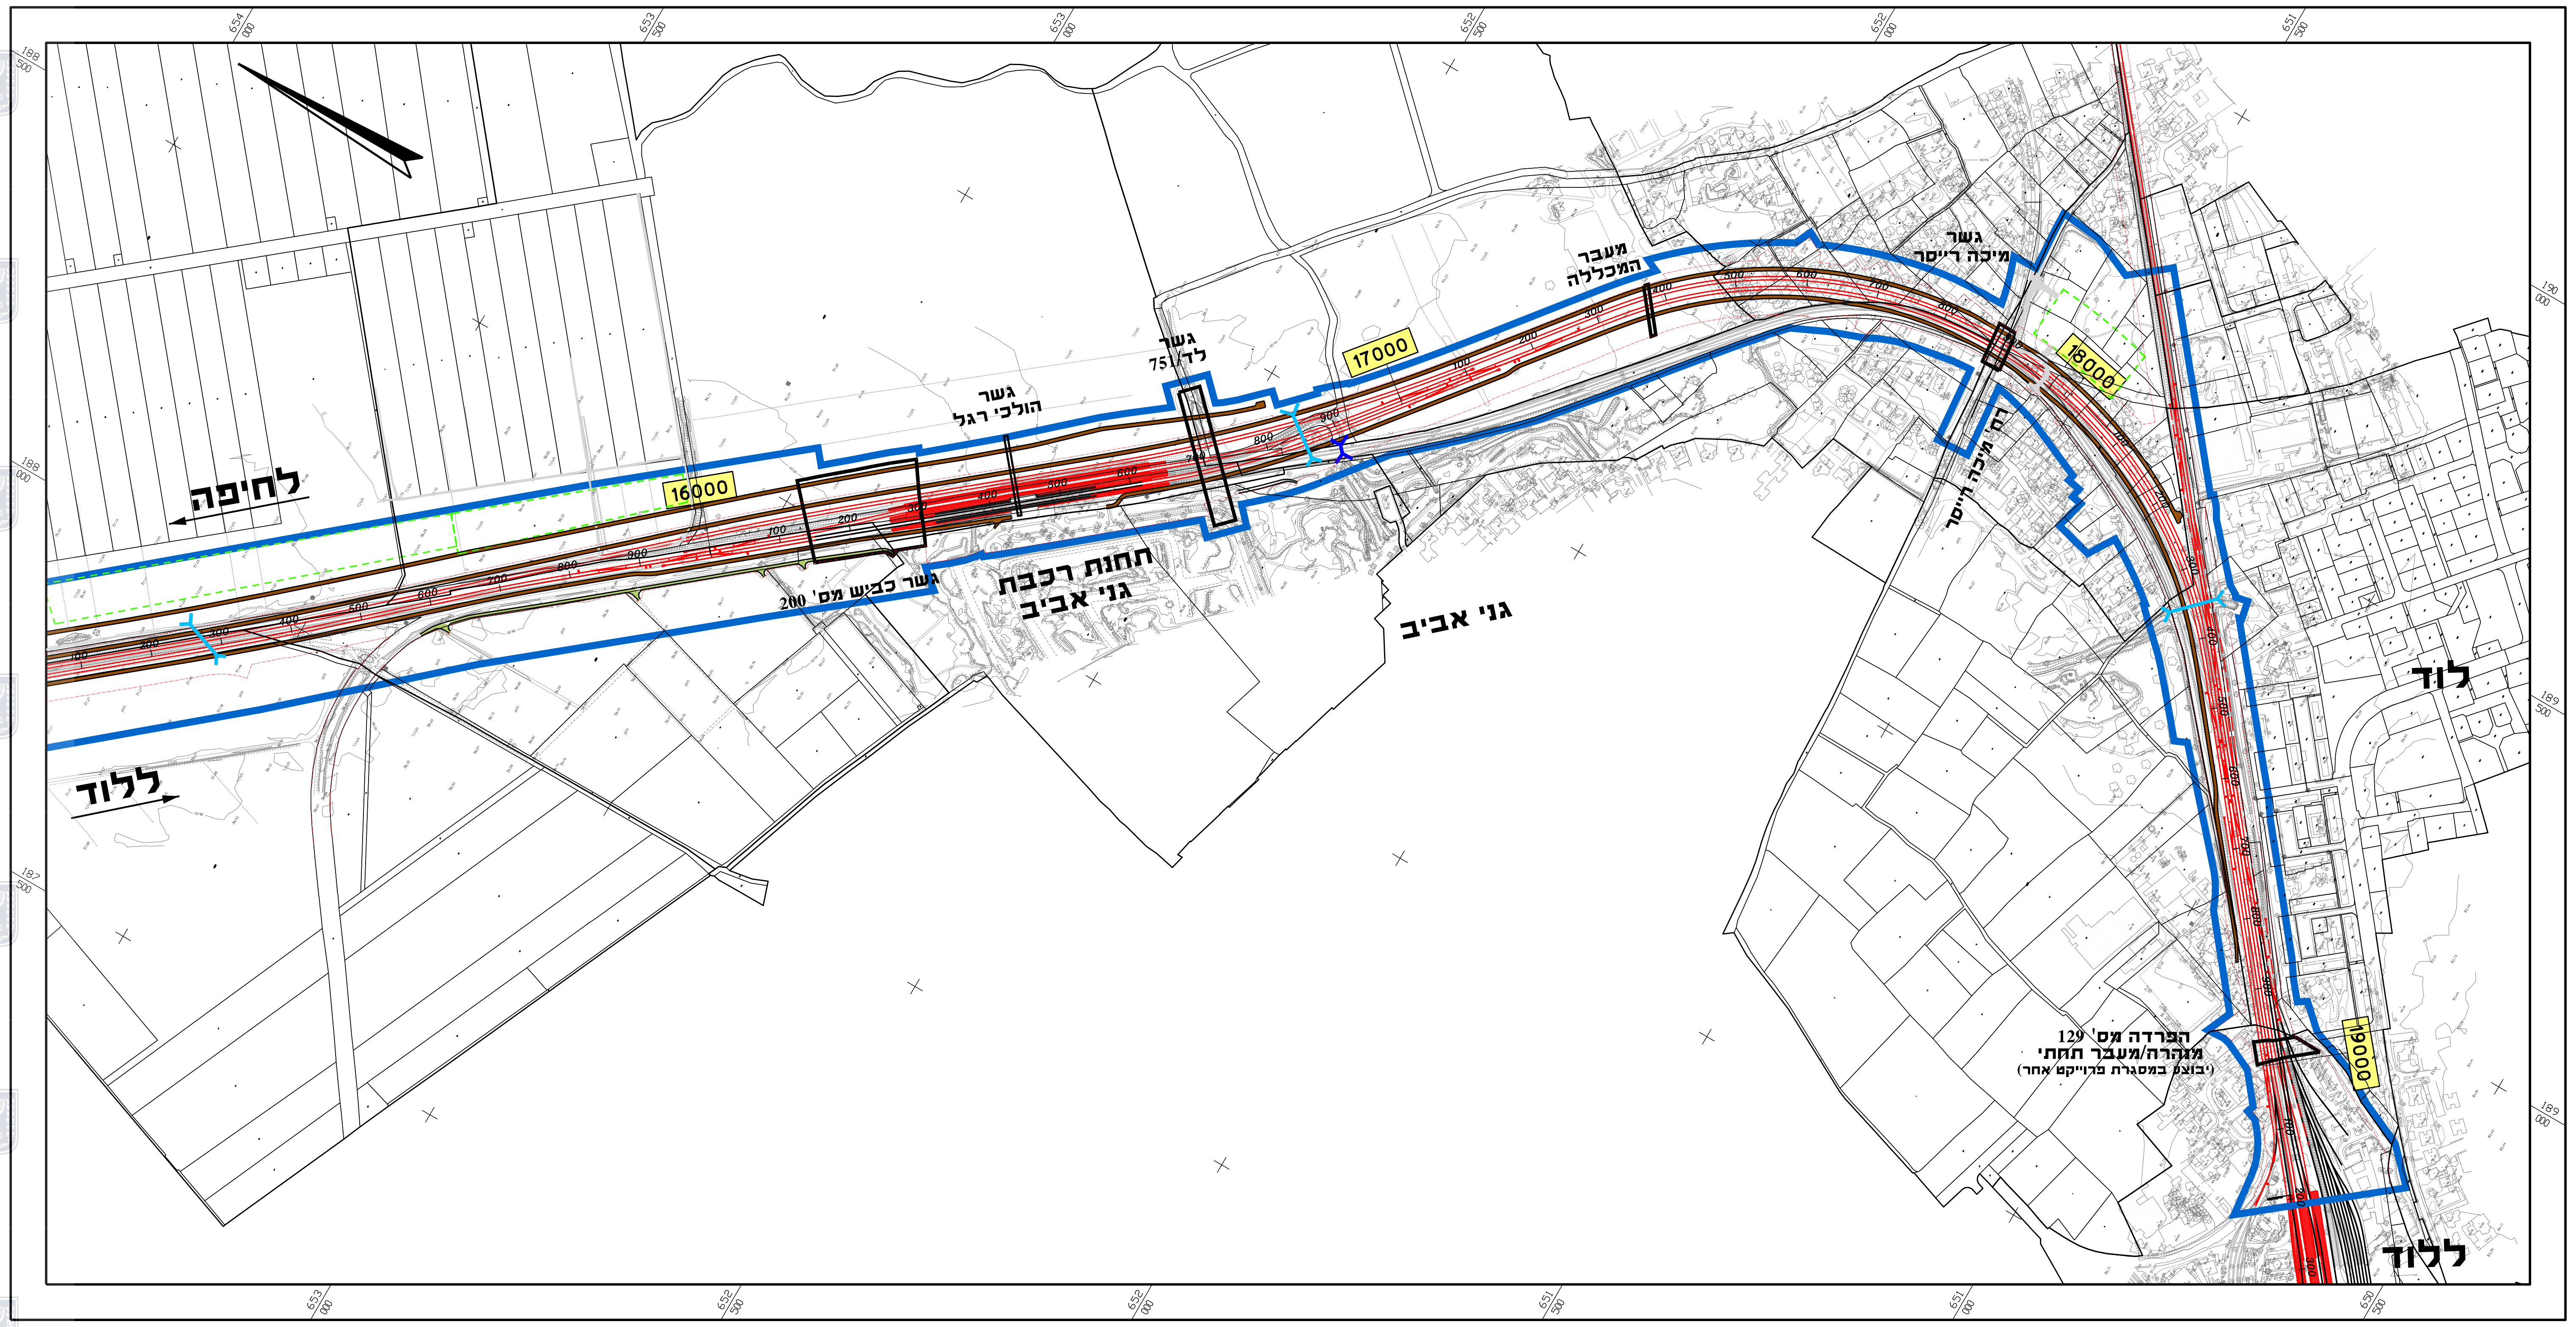

מקרא

גבול תכנית	
גבול רצועת רכבת מוצע	
גבול זכות הדרך	
גבול זכות נחל מתוכנן	
גבול גוש	
גבול חלקה	
מספר חלקה	205
מספר גוש	6974
ציר מסילה קיימת	
ציר מסילה מתוכננת	
מס׳ חתך\ק״מ	104000
גשר מתוכנן	
גשר\מעבר תת קרקעי מתוכנן	
מעביר מים קיים	
מעביר מים מתוכנן	
דרך שרות רכבת\ שרות כביש	
תעלת ניקוז\תעלת בטון	
אתר התארגנות	
דרכי גישה לאתרי התארגנות	

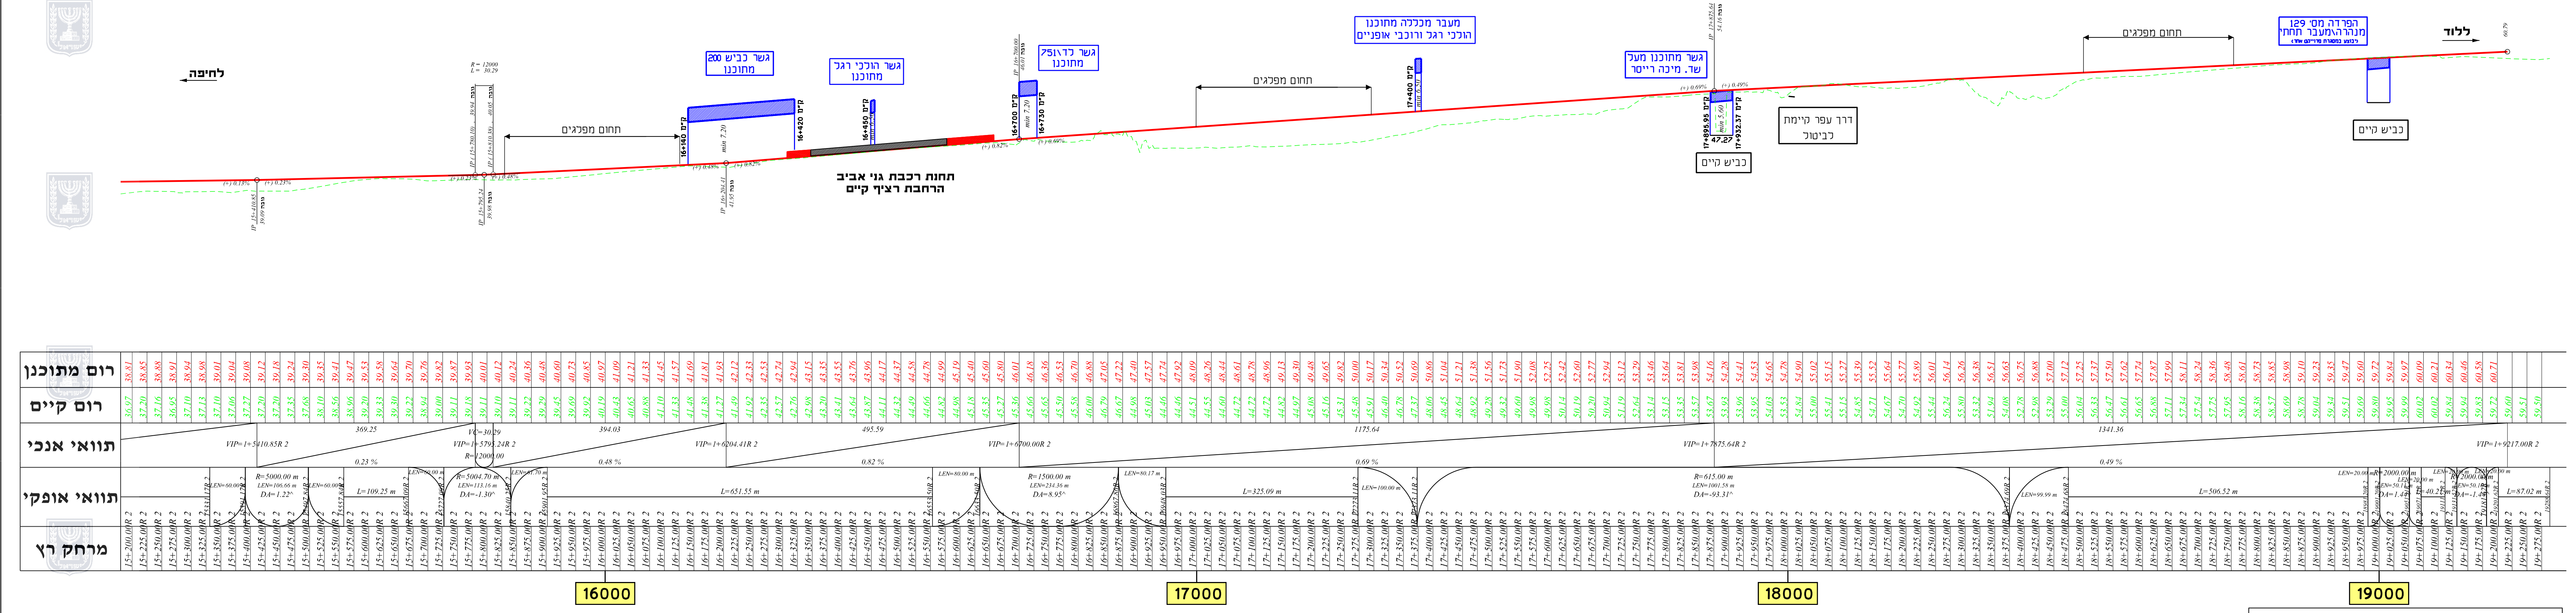

מקרא

מספר חתך\ק״מ	103000 104+000.00
גשר\מעבר תת קרקעי קיים	
גשר\מעבר תת קרקעי מתוכנן	
מעביר מים	M5 Box 1.5x1.2
רום קיים	
רום מתוכנן	
תחום מפלגים	
רציף קיים	
רציף מתוכנן	
רציף עתידי	

מדינת ישראל משרד האוצר הועדה הארצית לתכנון ולבנייה של תשתיות לאומיות	חתימה וחותמת				
בעלי קרקע מדינת ישראל ואחרים	חתימה וחותמת				
יוזמי התכנית נתיבי ישראל החברה הלאומית לתשתיות תחבורה בע"מ	חתימה וחותמת				
מנהל פרוייקט : יהל מהנדסים ייזום פרוייקטים בע"מ	חתימה וחותמת				
	שם: איתי עובדיה	תפקיד: מנה"פ	מס' ת"ז 023518210	כתובת: רח. יגאל אלון 67 , תל אביב	
	טלפון: 03-6251222	פקס: 03-6251223	דוא"ל: itay@yahel-eng.co.il	שם:	
עורך התוכנית ינון תכנון יעוץ ומחקר בע"מ הנדסה אזרחית, דרכים, תנועה, מסילות ברזל, אדר' נוף ומבנים, הדמיות, קונסטרוקציות, מדידות וניהול פרויקטים	חתימה וחותמת				
	שם: אלכס לרנר	תפקיד: מתכנן	מס' ת"ז 308640283	כתובת: רח. היוזמה 4 , טירת הכרמל	
	טלפון: 04-8569000	פקס: 04-8569010	דוא"ל: yenon@yenon.co.il	שם: ינון-תכנון יעוץ ומחקר בע"מ	
מודד מוסמך קבוצת דטהמפ DATAMAP GROUP דטהמפ אגרומפ איזומפ גטניר ושות' רח' הירקון 67, בני-ברק 51206 טל.03-7541000 פקס.03-7516356 67 Hayarkon St. Bnei-Brak 51206 Tel.03-7541000 Fax.03-7516356	חתימה וחותמת				
	שם: ברנרד גטניו	מודד מוסמך 570	מס' ת"ז 052602984	כתובת: רח. הירקון 67 , בני ברק	
	טלפון: 03-7541000	פקס: 03-7516353	דוא"ל: info@datamap.com	שם:	

הריני מצהיר בזאת כי מדידת המפה הטופוגרפית/המצבית המהווה רקע לתוכנית זו, נערכה על ידי ביום __________
והיא הוכנה לפי הוראות נוהל מבא"ת ובהתאם להוראות החוק ולתקנות המודדים שבתוקף.
דיוק הקו הכחול והקדסטר: מדידה גרפית/ קו כחול (בלבד) ברמה אנליטית/ מדידה אנליטית מלאה ברמת תצ"ר (כולל הקו הכחול)

שם המודד ______ מספר רישיון ______ חתימה ______ תאריך ______